

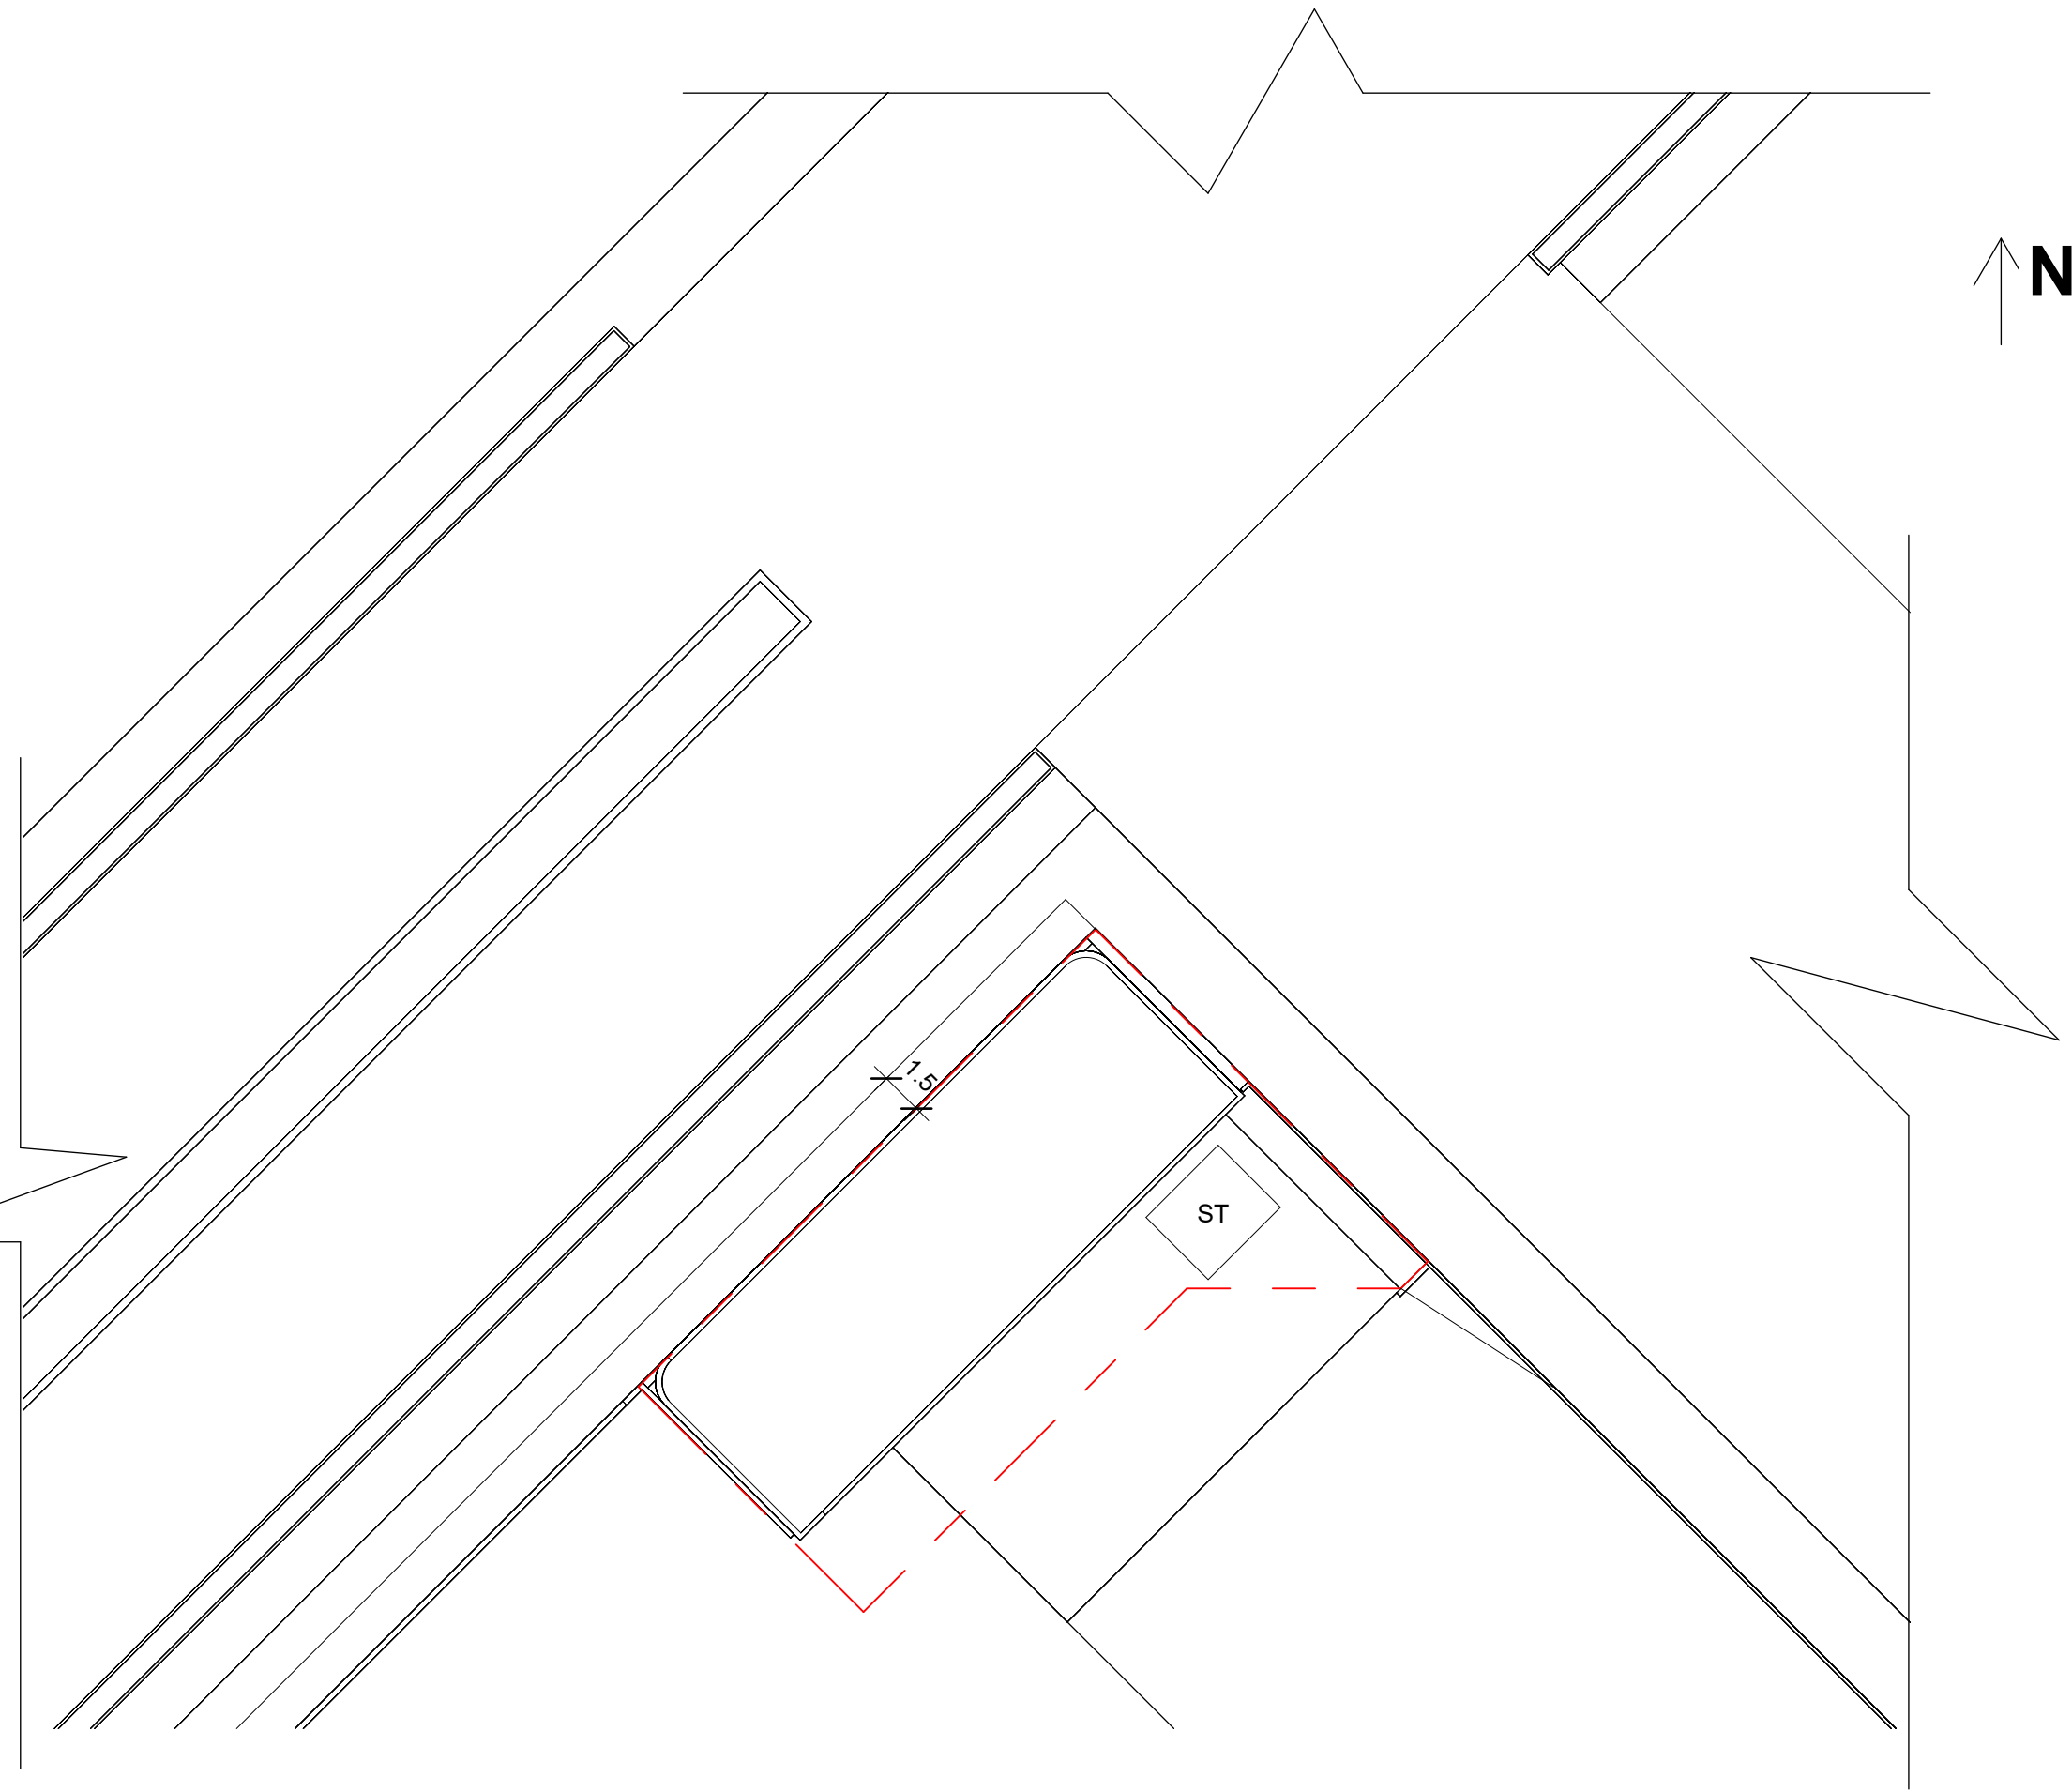
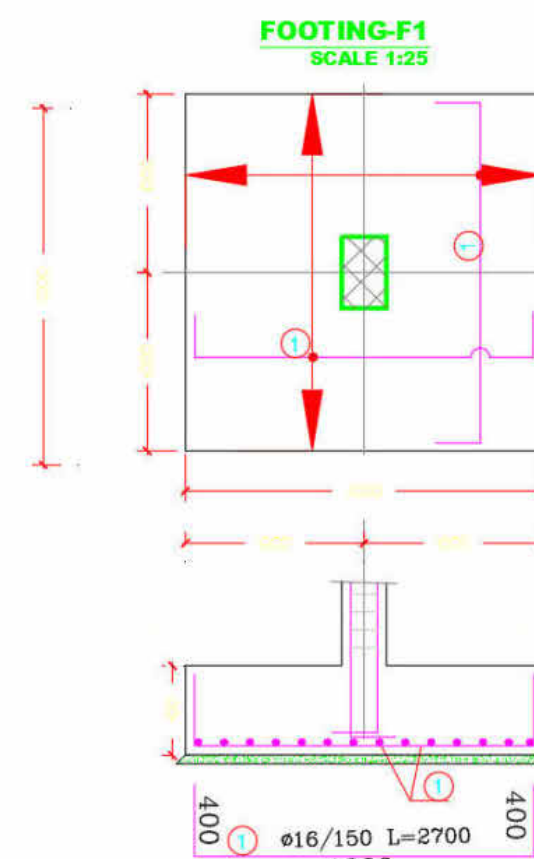
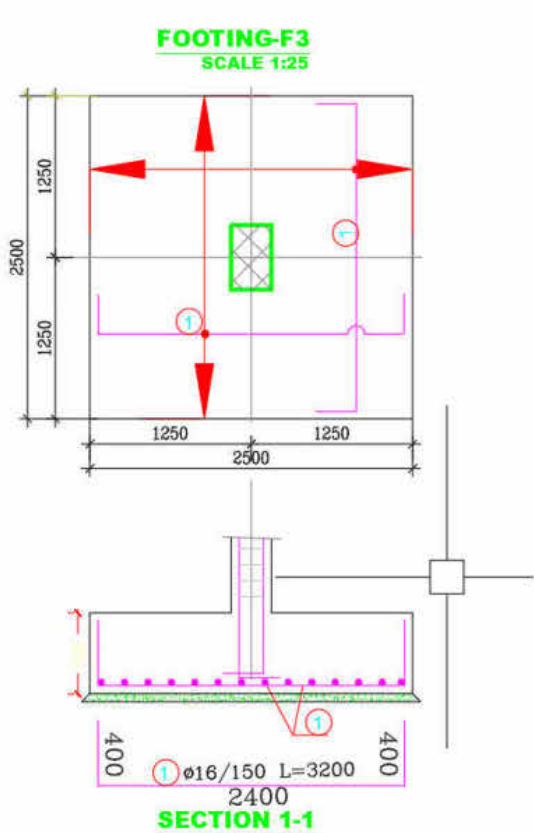
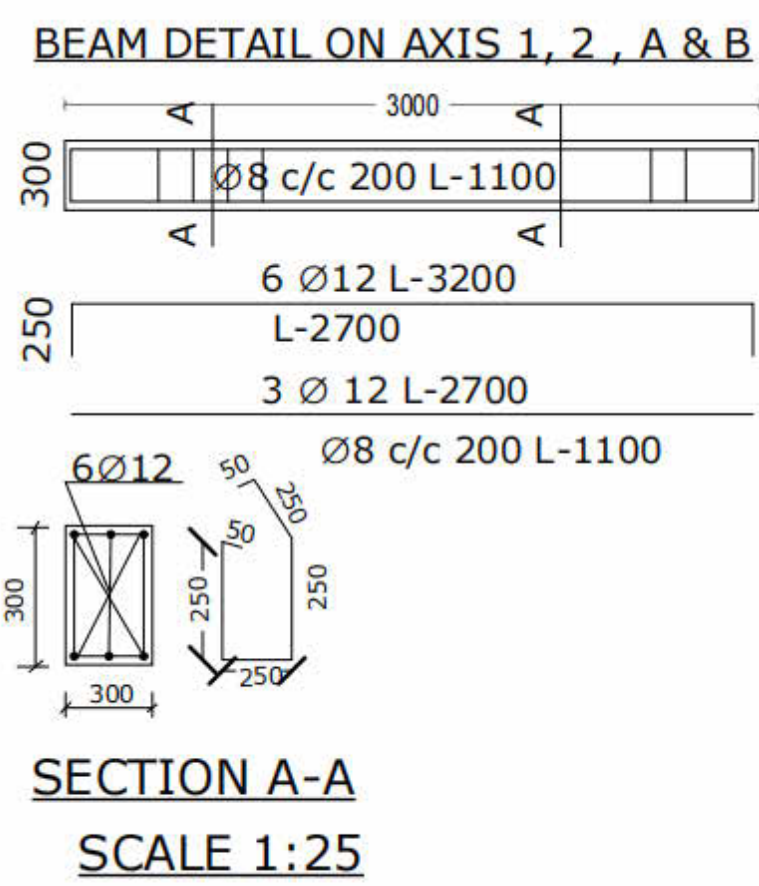
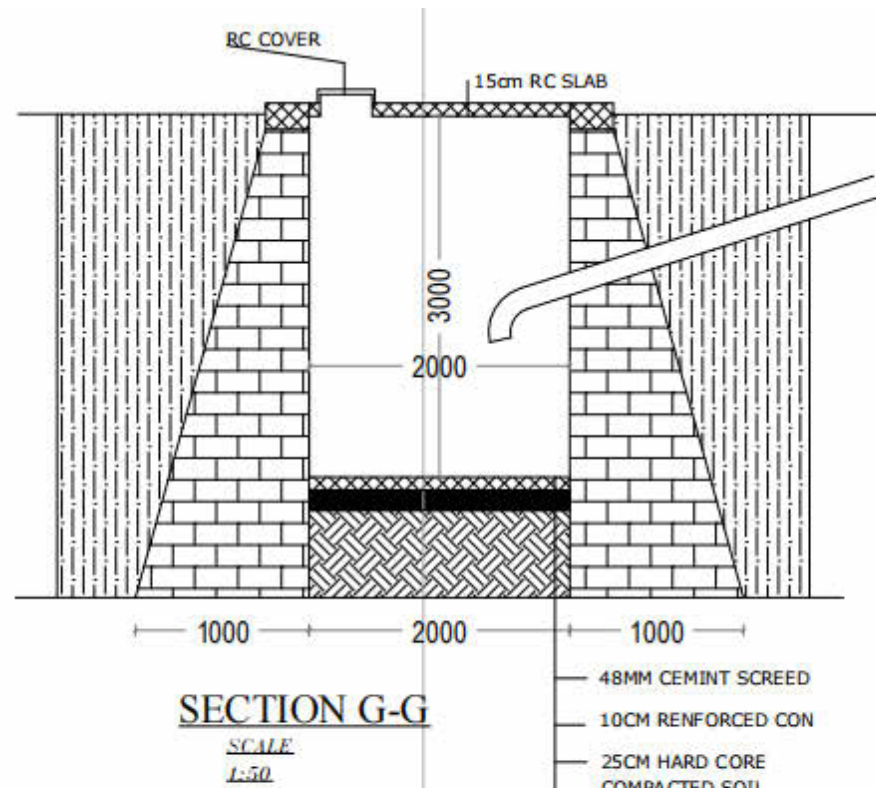
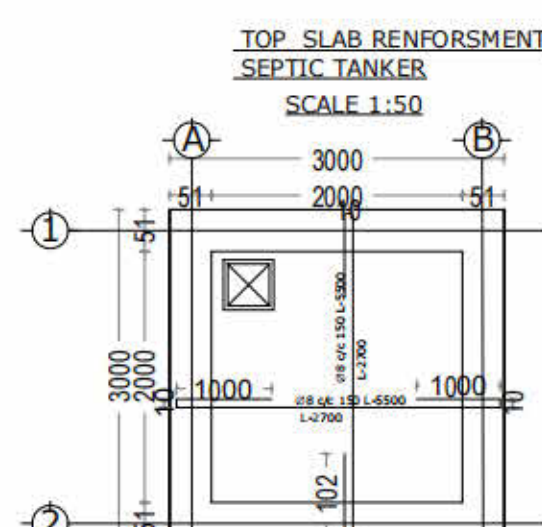
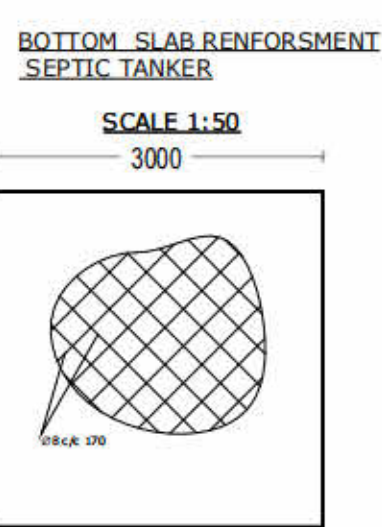



5 Site
1 : 250

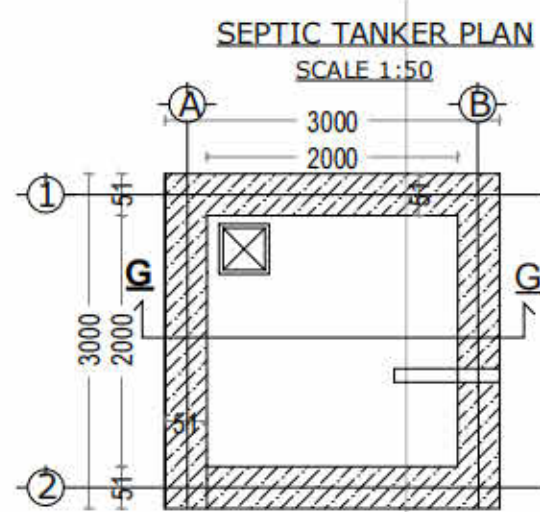


7 Section X
1 : 100

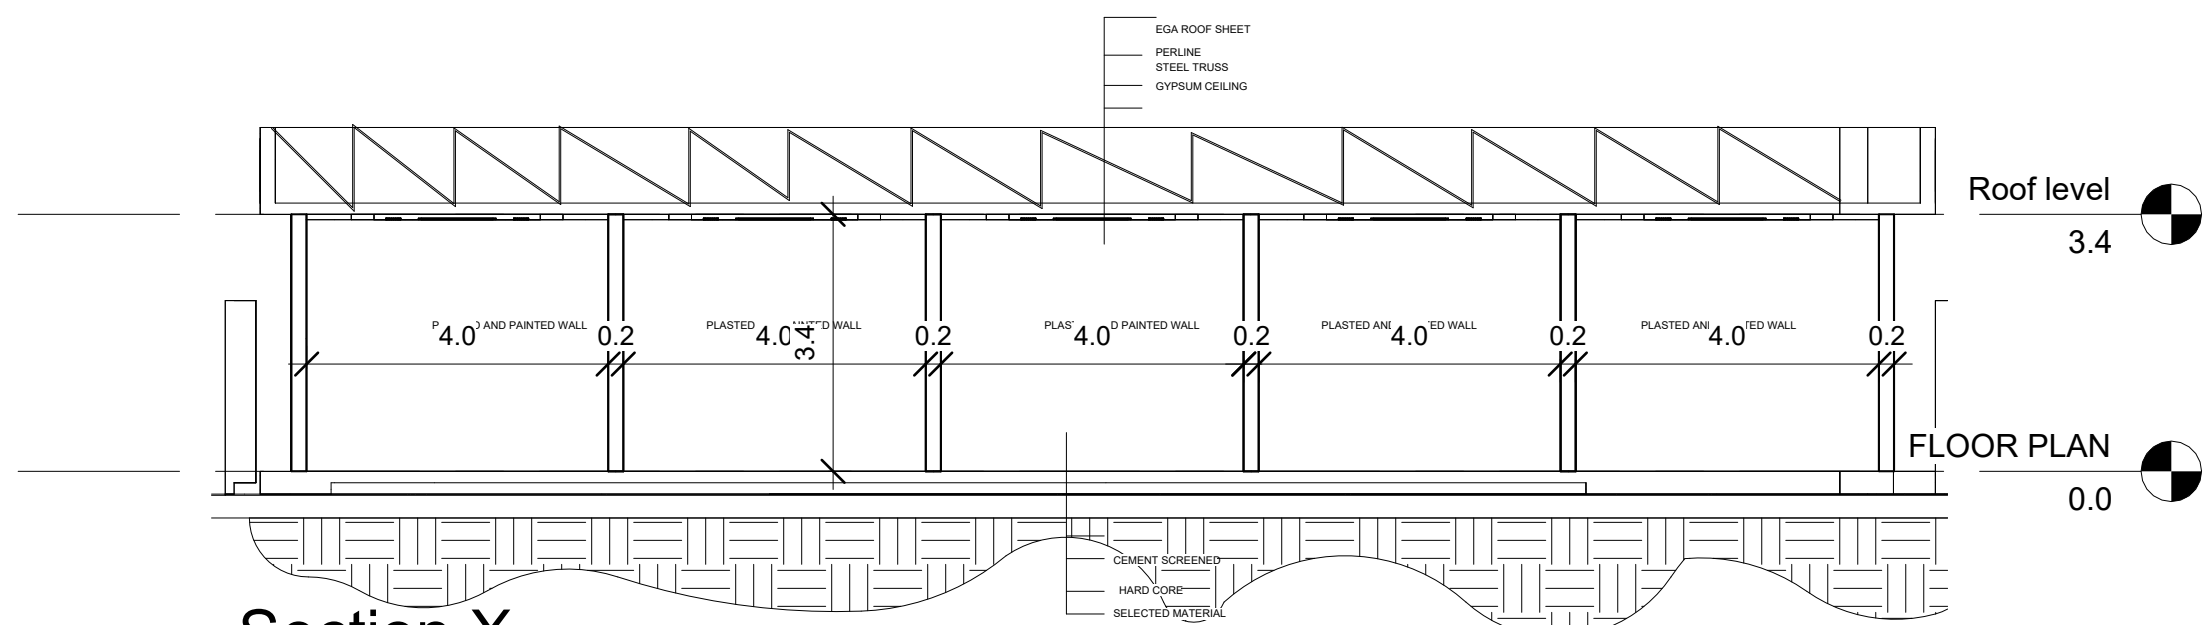


6 FLOOR PLAN
1 : 100

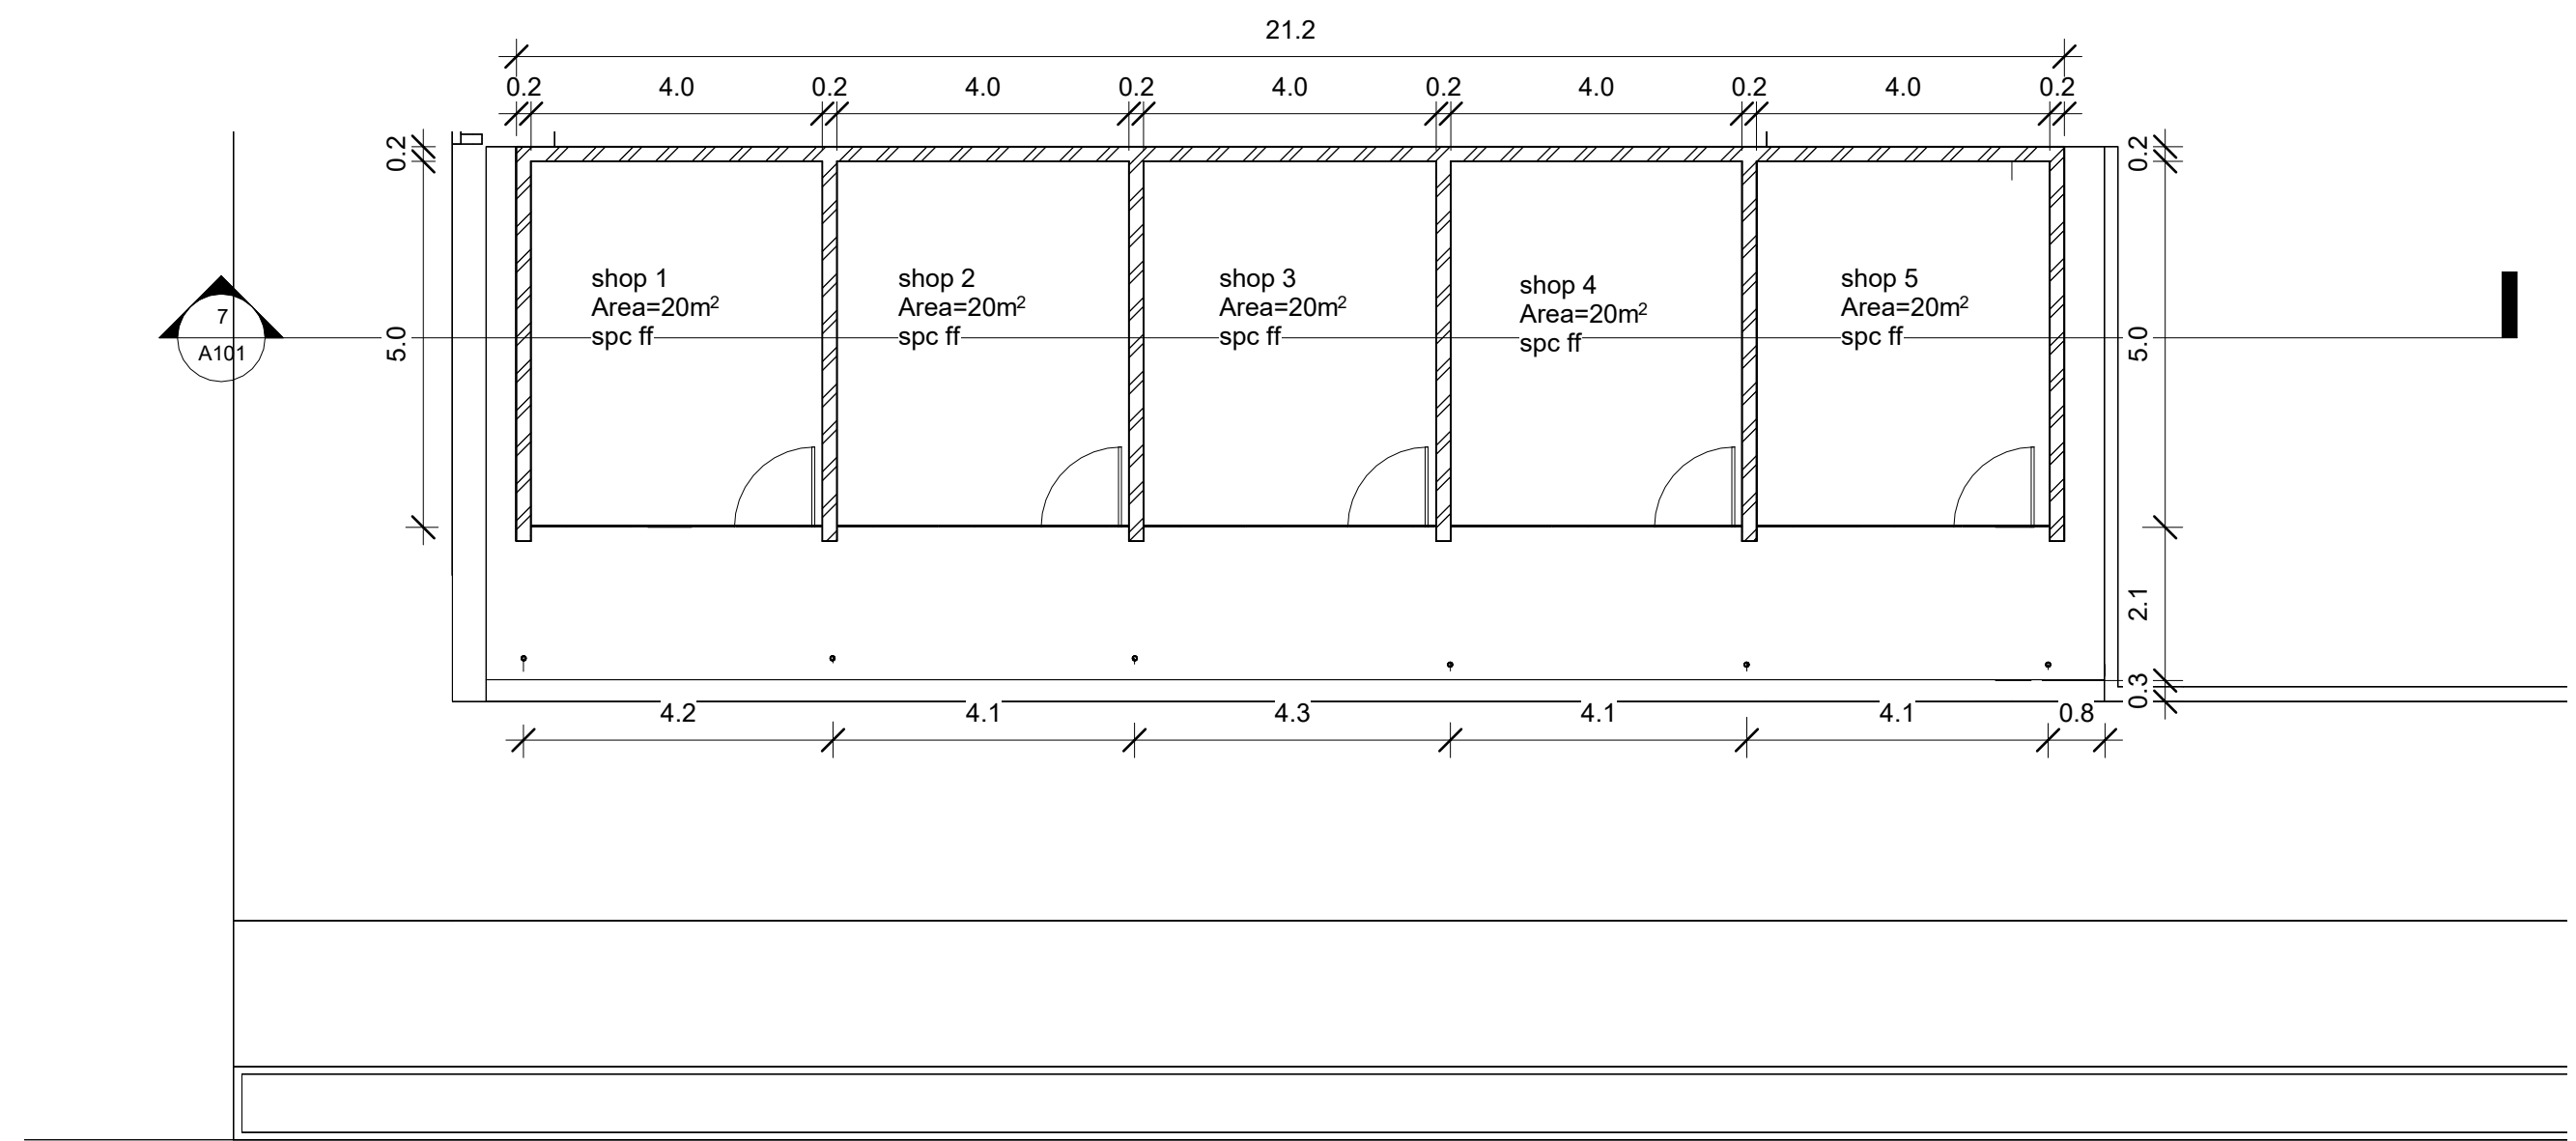


2 FRONT ELEVATION
1 : 100

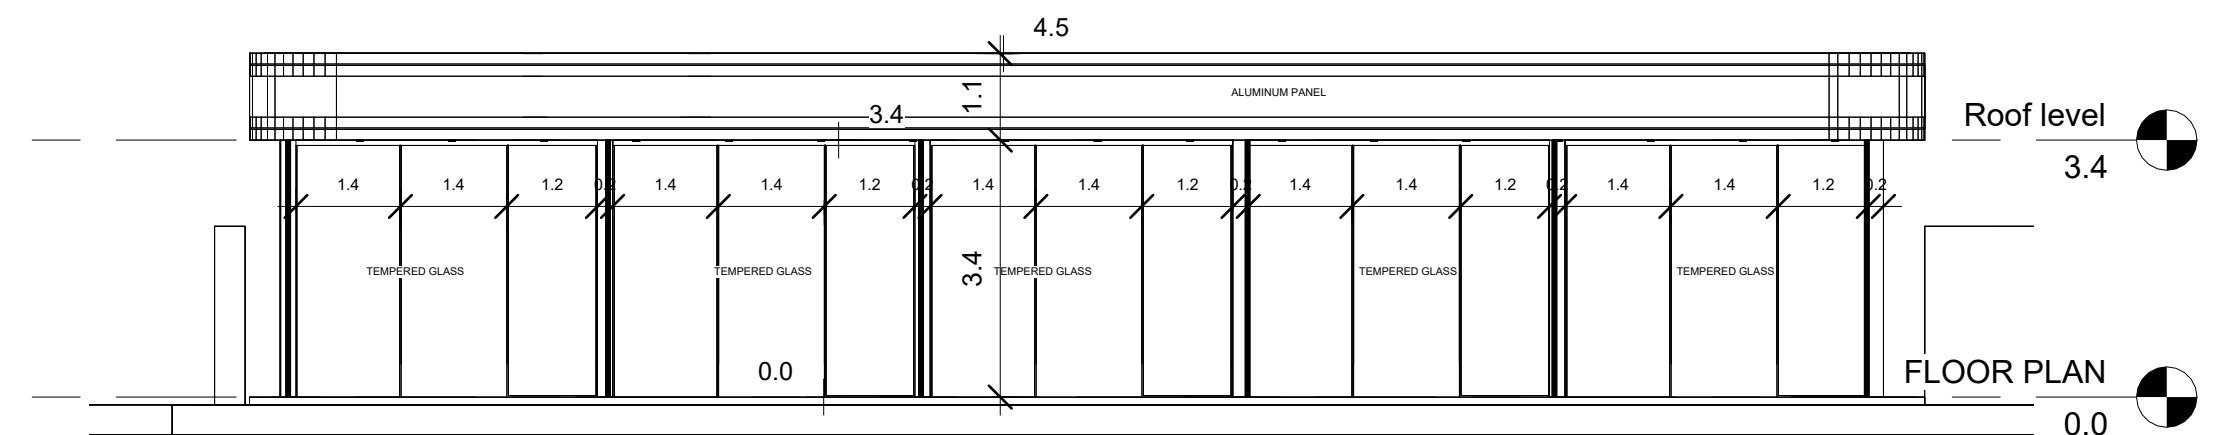


3 REAR ELEVATION
1 : 100

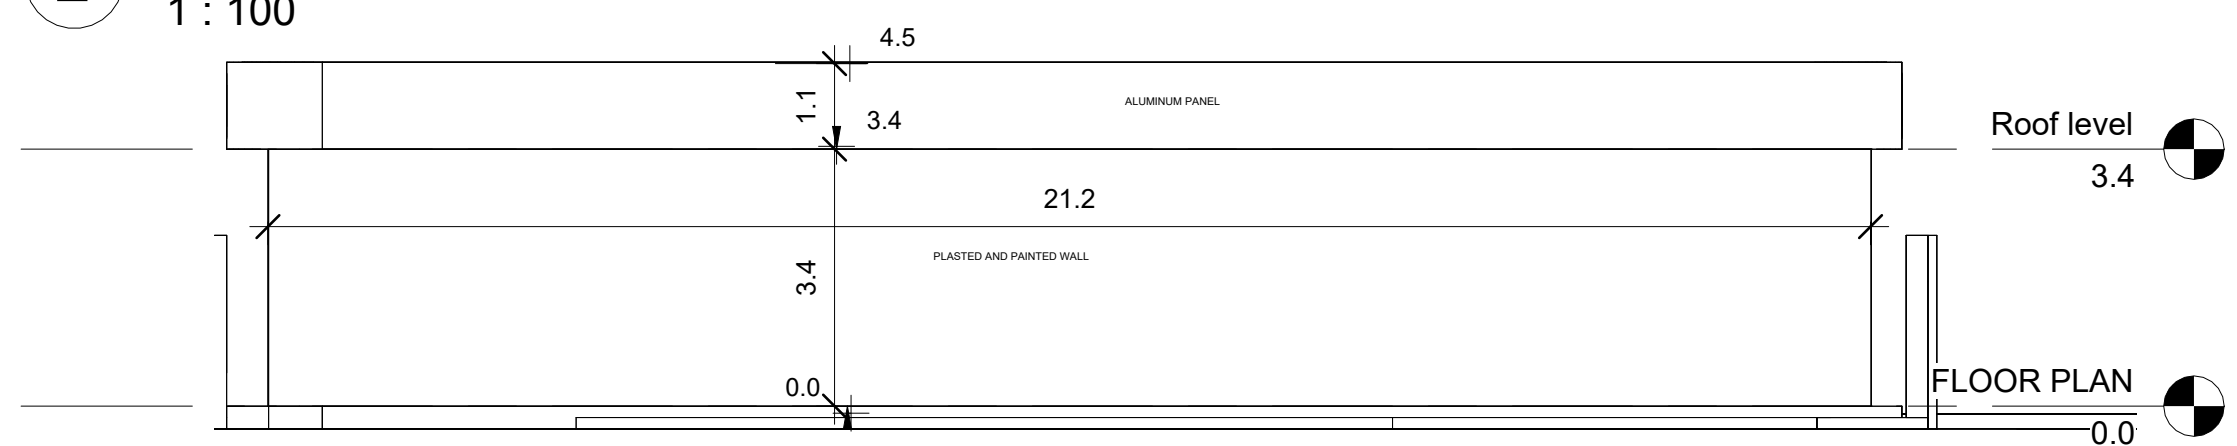

4 LEFT ELEVATION
1 : 100

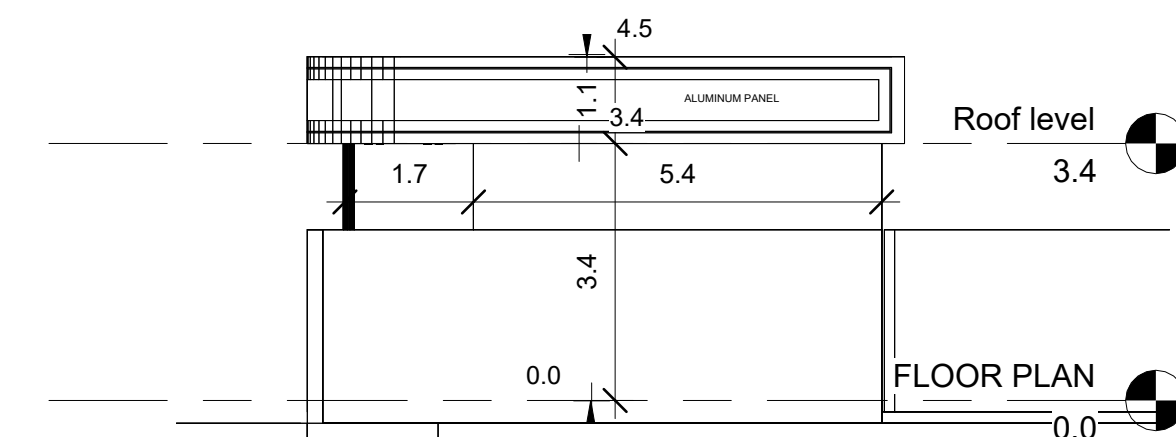


1 RIGHT ELEVATION
1 : 100

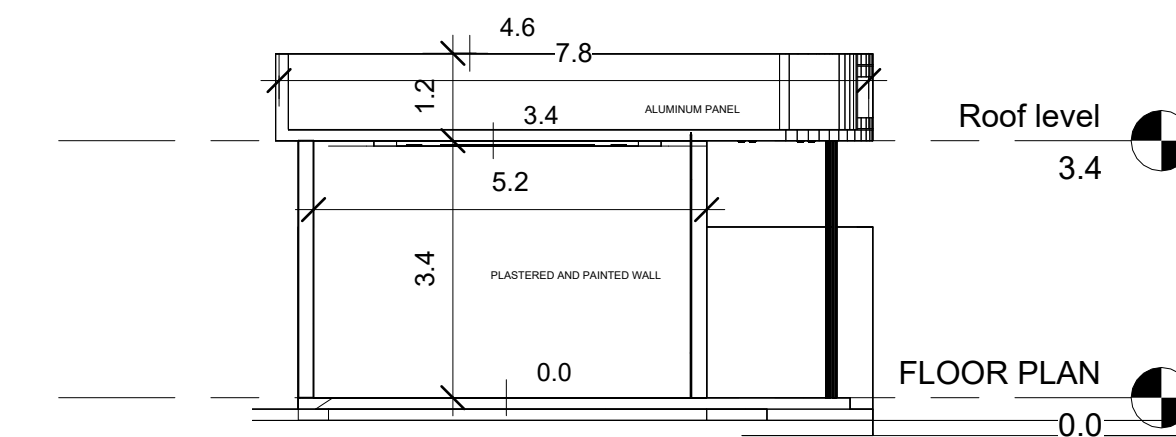


Genekibo Architects

CLIENT	AREDO ESSIE		
LOCATION	SEMERA		
	NAME	REG.	
DESIGN BY	HABIB AHMED	GAR/88764	
CHECKED BY	MOHAMMED ABDELAH	GAR/96320	
APPROVED BY	MOHAMMED ABDELAH	GAR/96320	
DESIGN REF.			
PROJECT	Shoping Center		
DRAWING TITLE	ARCHITECTURAL DRAWING		
SCALE	AS INDICATED		
DATE	6/09/2026		

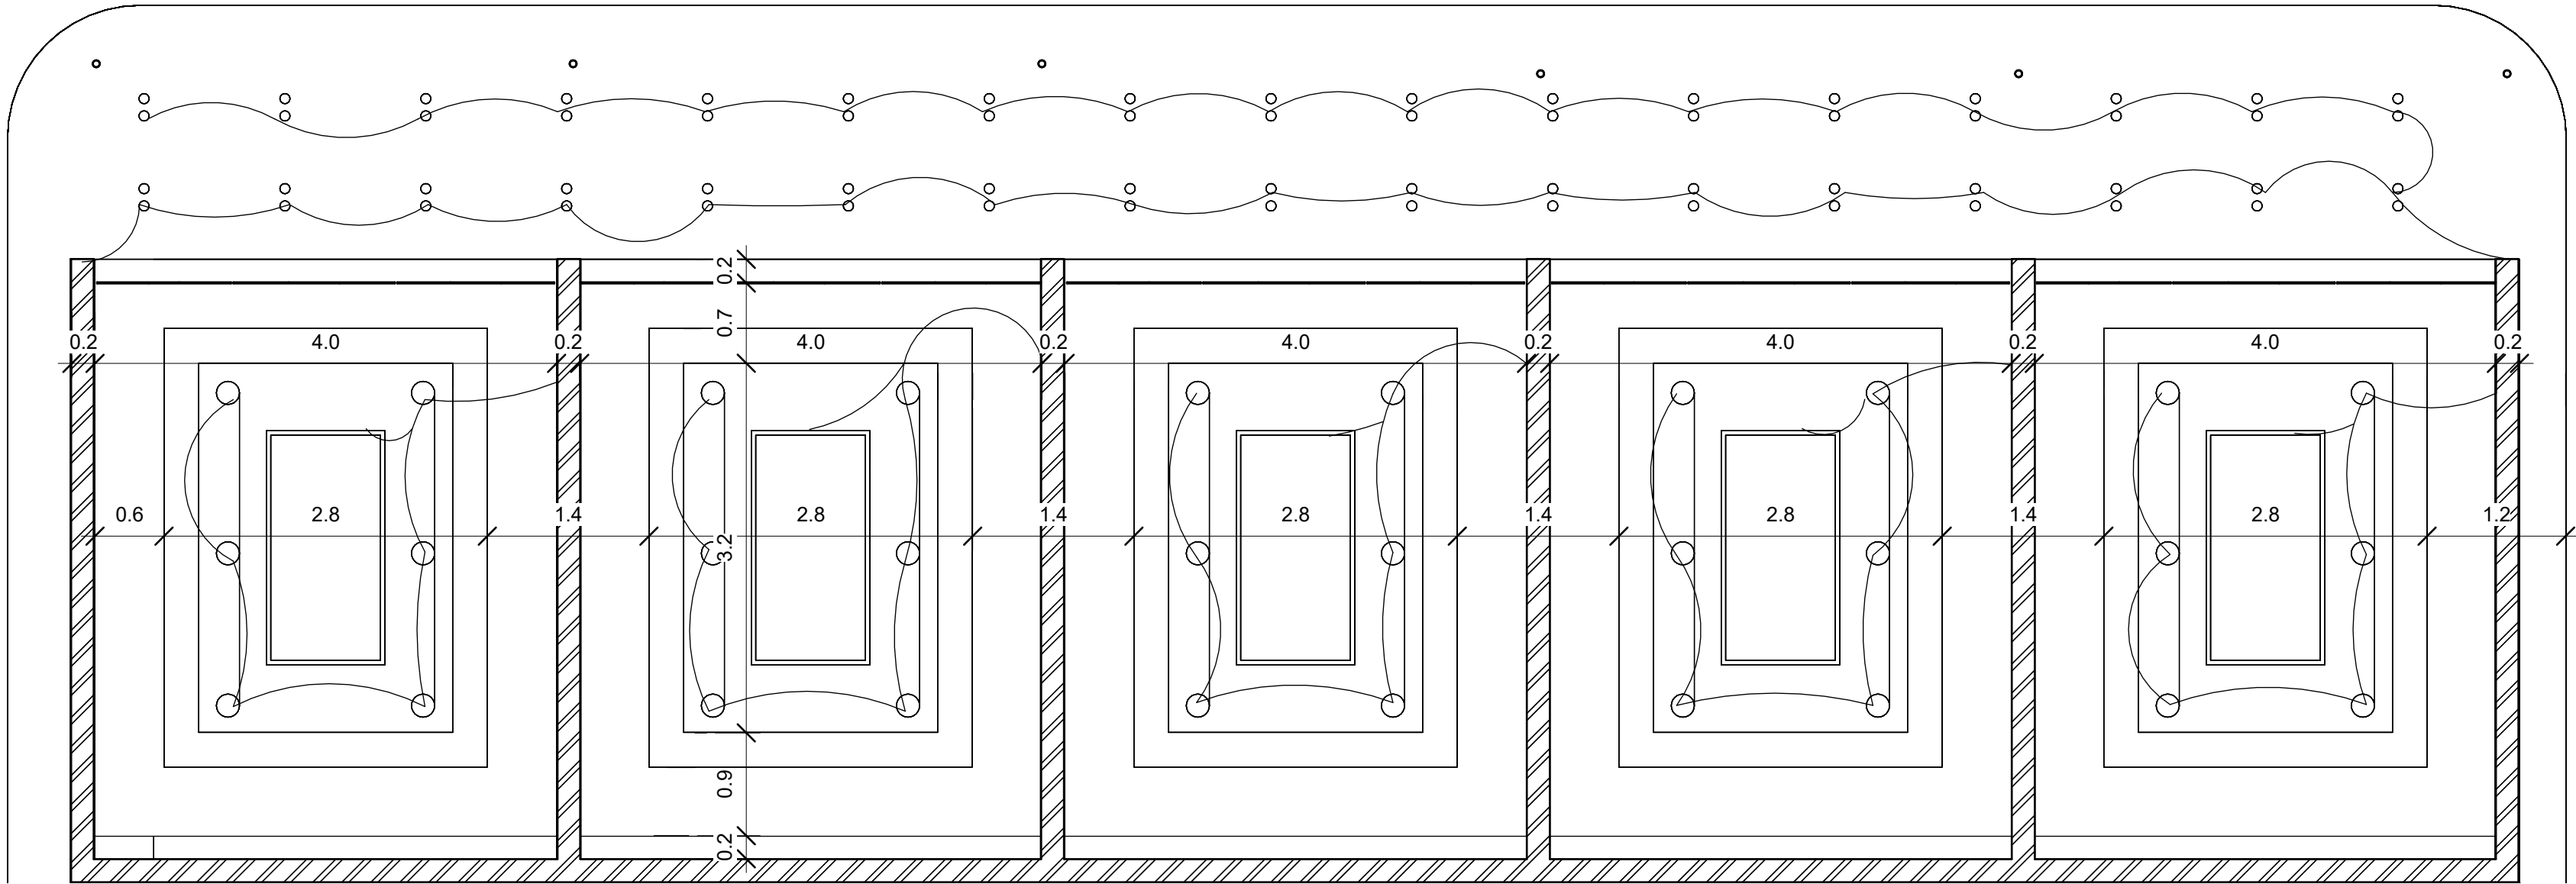

1
1:50

INSTALLATION OF LIGHT
AND SWITCH

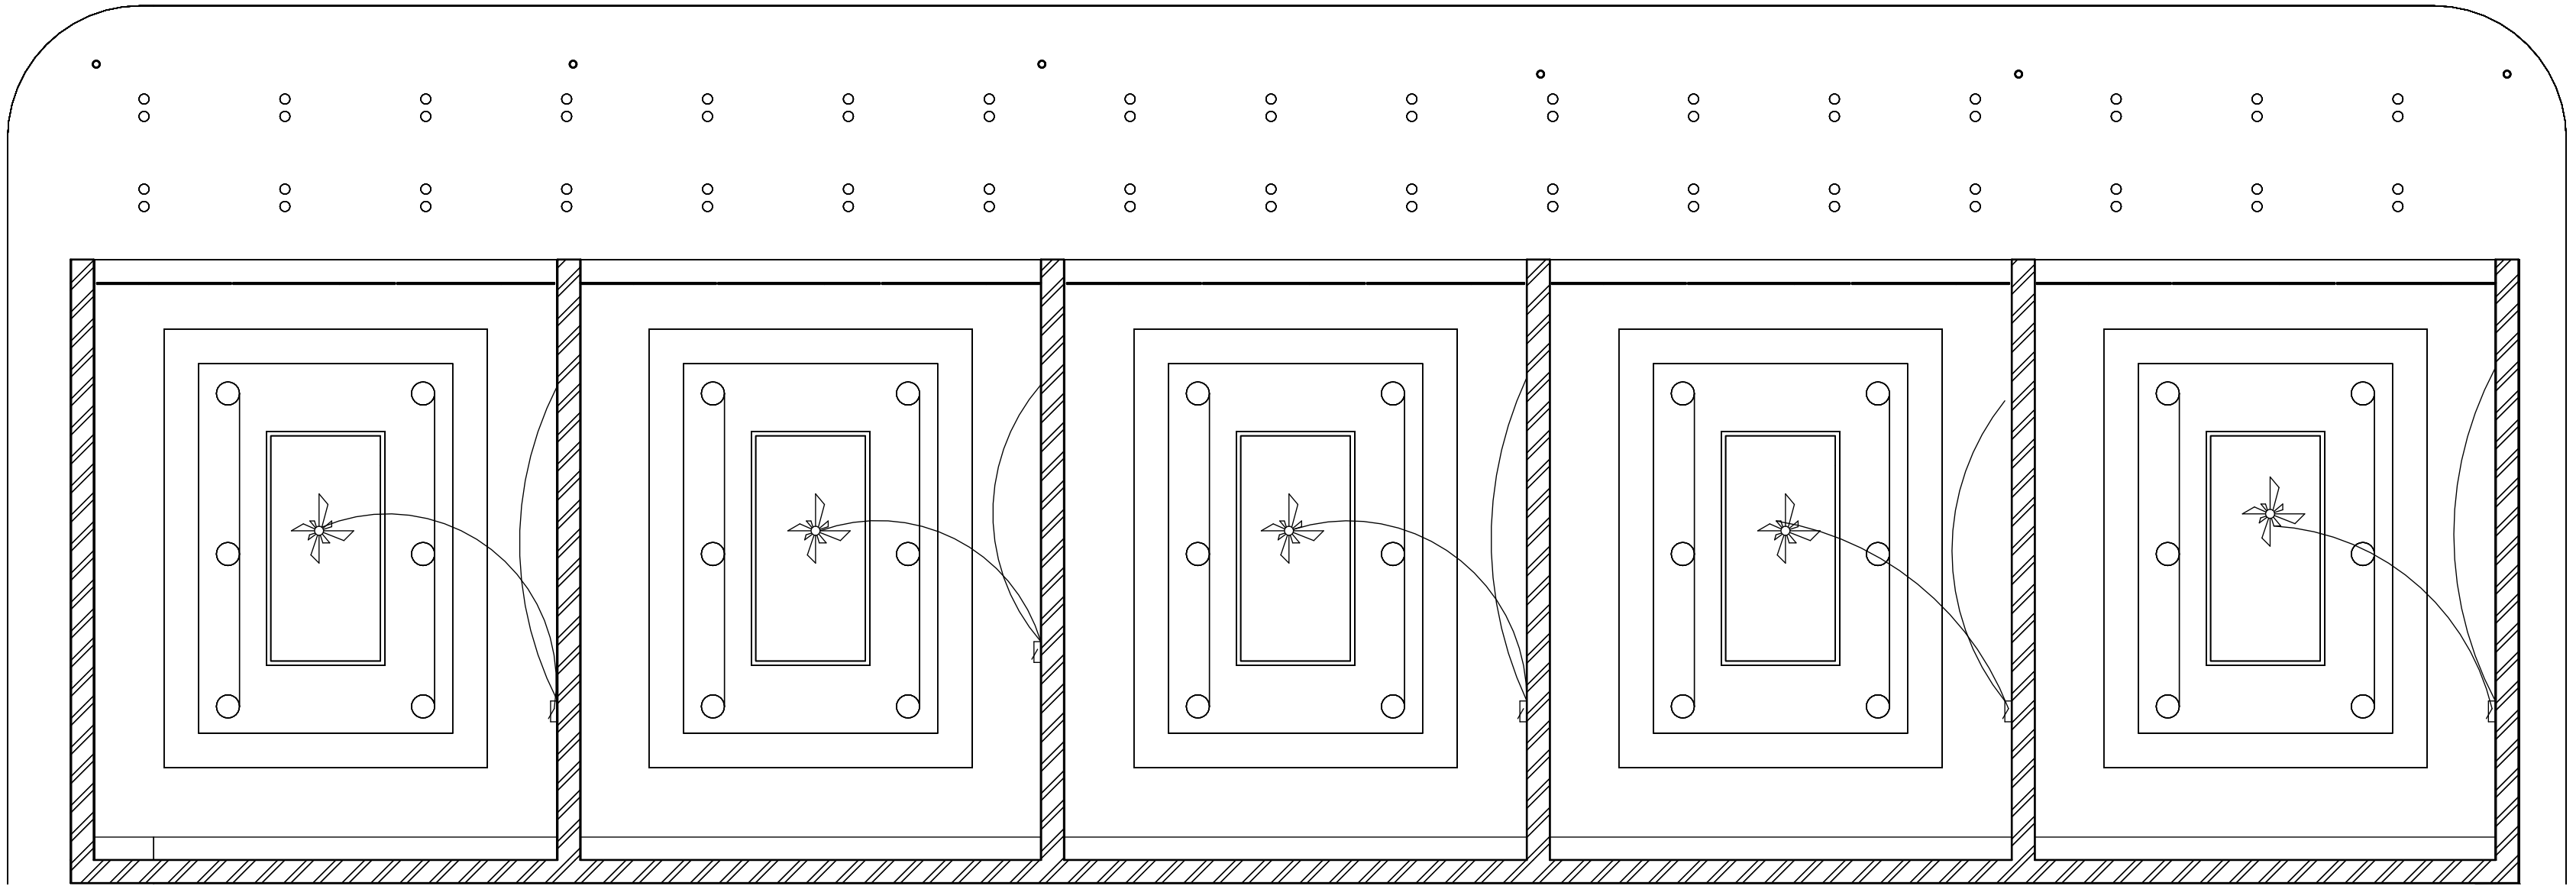


2
1:50

INSTALLATION OF SOCHET
AND FAN

LEGEND

- SURFACE MOUNTED DOWN LIGHT
- SURFACE MOUNTED WALL LIGHT
- PEDESTAL & POST TOP LIGHT
- RECESSED MOUNTED SINGLE SWITCH
- RECESSED MOUNTED TWO-WAY SWITCH
- RECESSED MOUNTED DOUBLE SWITCH
- RECESSED MOUNTED SINGLE SOCKET OUTLET
- RECESSED MOUNTED TV OUTLET
- RECESSED MOUNTED WATER PROOF SINGLE SOCKET OUTLET
- RECESSED MOUNTED HEATER OUTLET
- Distribution Board
- Wall Mounted Light Fitting
- TV Outlet
- TV Coaxial Cable inside conduit of Ø 19mm
- Flush Mounted TV Terminal Box
- Telephone Voice or Data Outlet RJ45 (Mounting Height @30cm FFFL)
- Rack Mounted Telephone Terminal Box and/or Data Switch
- Flush Mounted Telephone(Only Voice) Terminal Box
- Data CAT 6A Cable inside conduit of Ø 19mm

DESCRIPTION	I(A)	A(mm)	P(KW)	R	S	T	Conduit dia.(mm²)
LIGHTING	1/10A	2x2.5	0.445	●			13
LIGHTING	1/10A	2x2.5	0.385		●		13
SOCKET OUTLET	1/16A	3x2.5	1.00			●	16
SOCKET OUTLET	1/16A	3x2.5	1.20	●			16
SOCKET OUTLET	1/16A	3x2.5	1.20		●		16

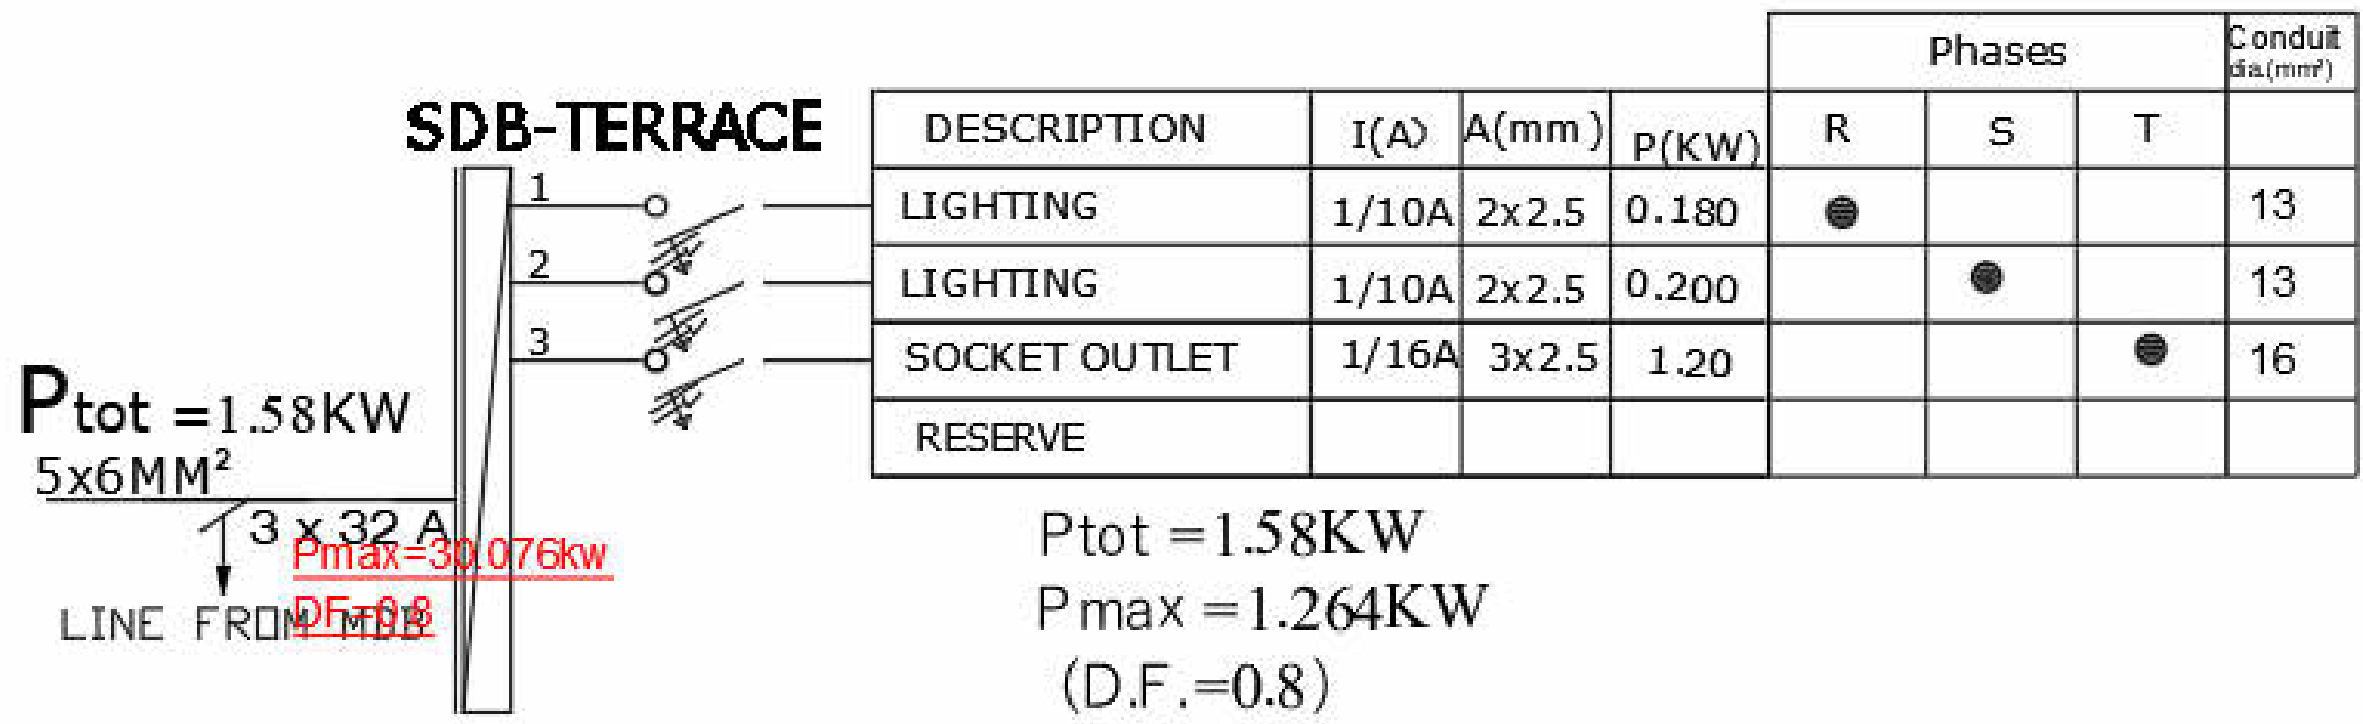

Genekibo Architects

CLIENT	AREDO ESSIE		
LOCATION	SEMERA		
	NAME	REG.	
DESIGN BY	HABIB AHMED	GAR/88764	
CHECKED BY	MOHAMMED ABDELAH	GAR/96320	
APPROVED BY	MOHAMMED ABDELAH	GAR/96320	
DESIGN REF.			
PROJECT	Shoping Center		
DRAWING TITLE	ELECTRICAL DRAWING		
SCALE	AS INDICATED		
DATE	6/09/2026		