


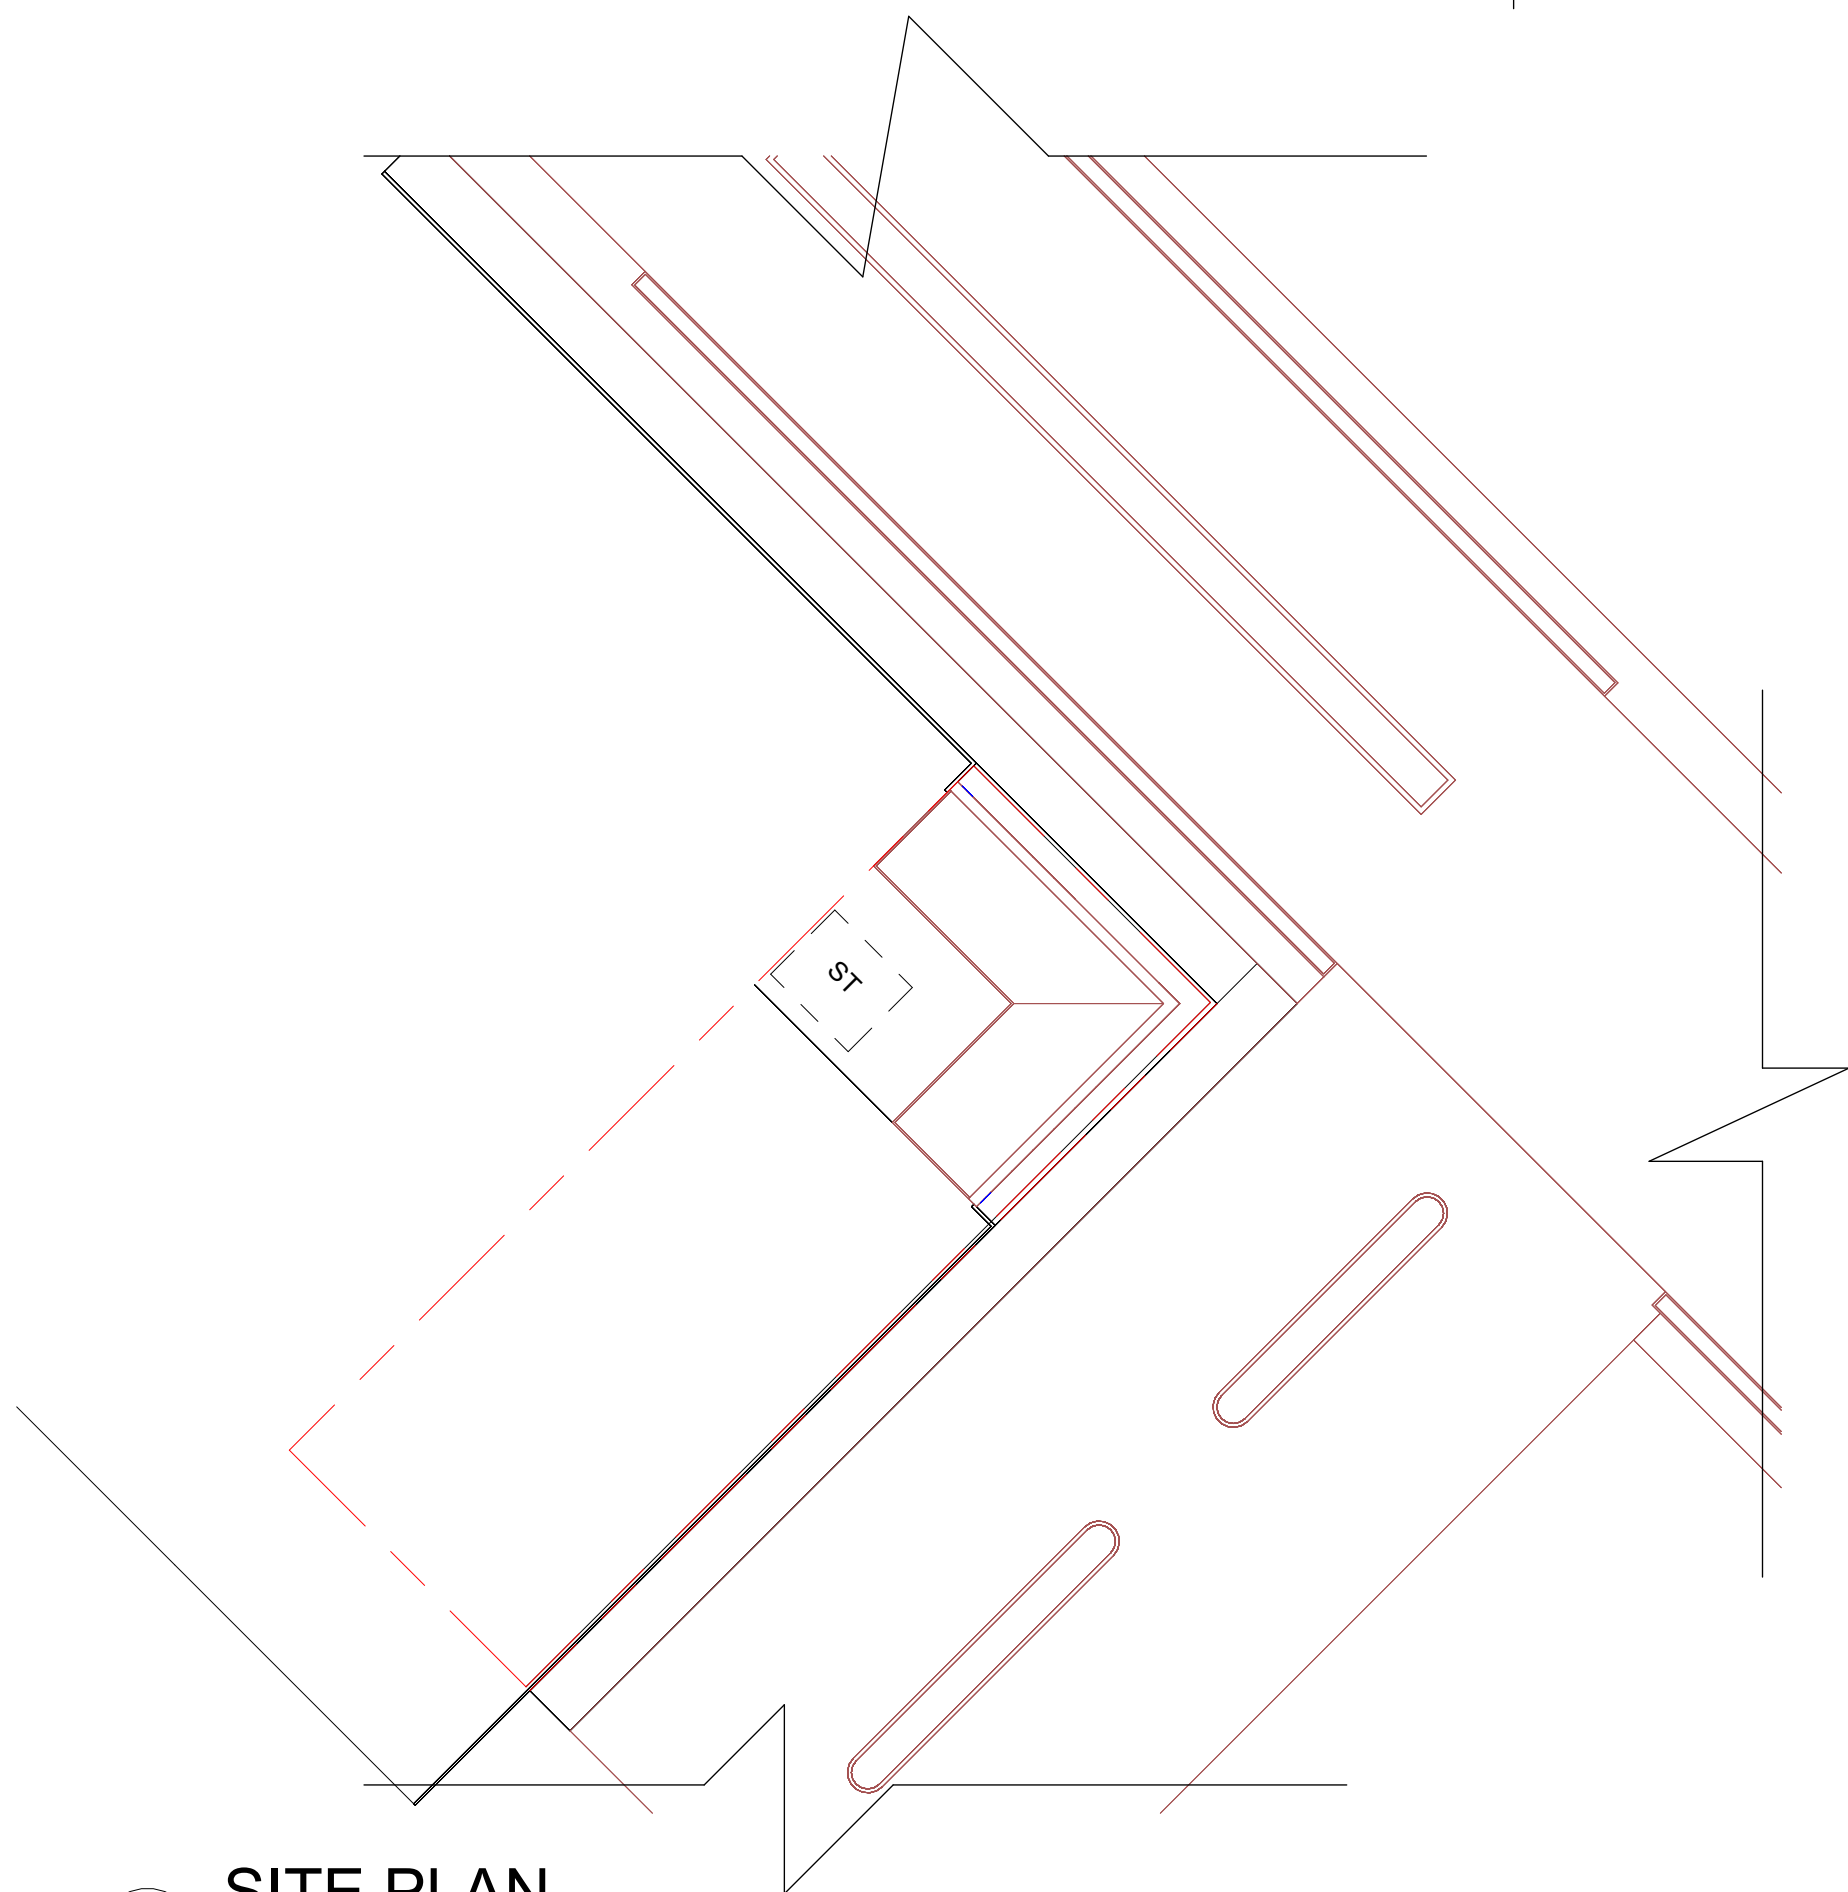
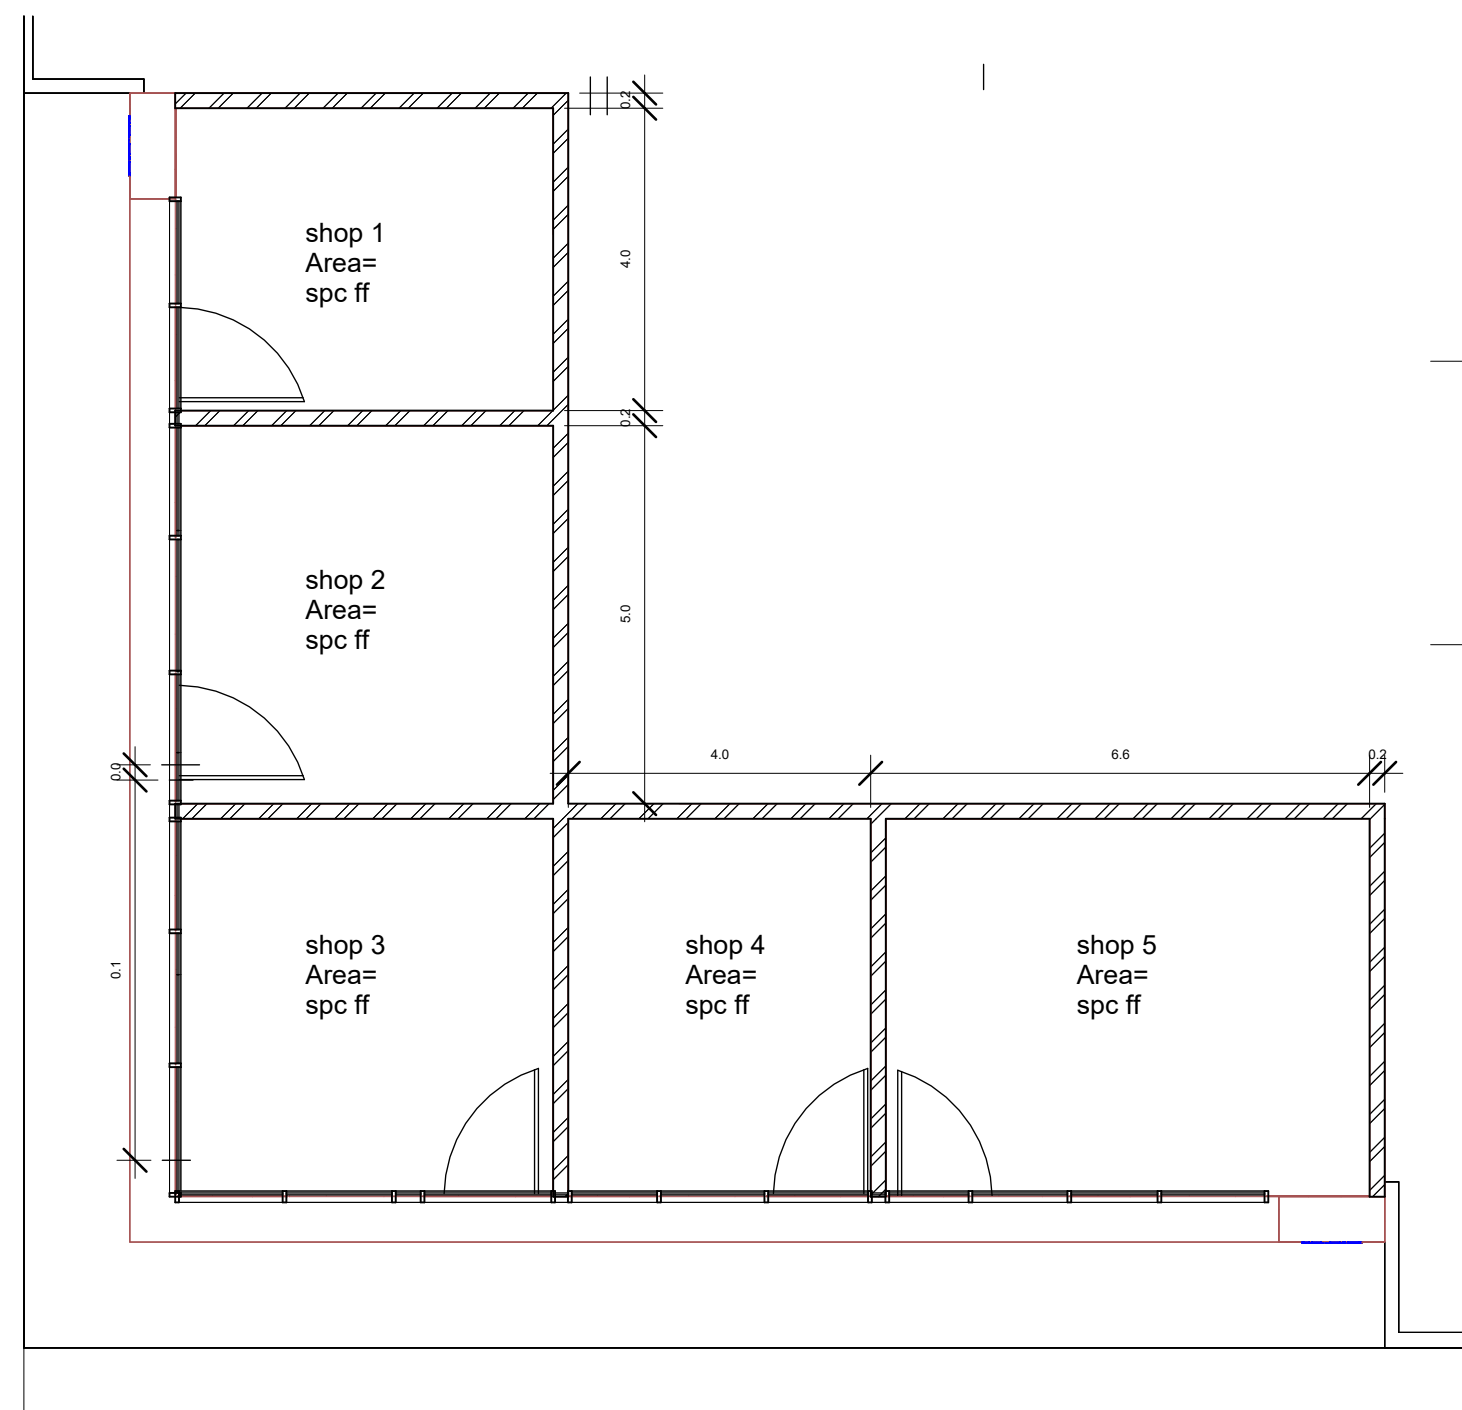
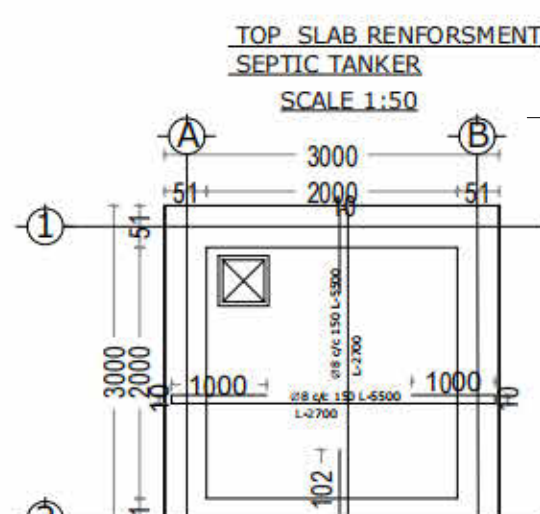


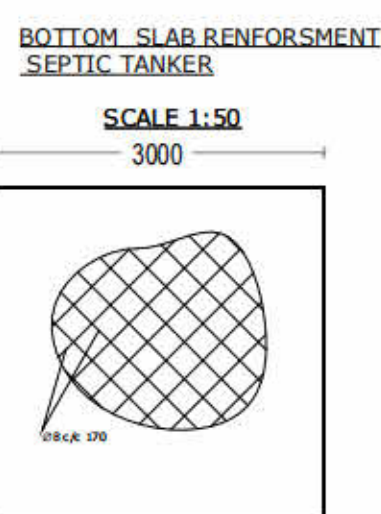



5 SITE PLAN
1 : 400

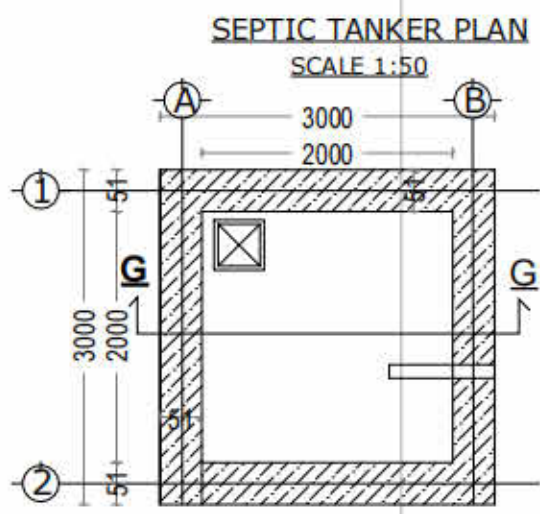


6 FLOOR PLAN
1:100

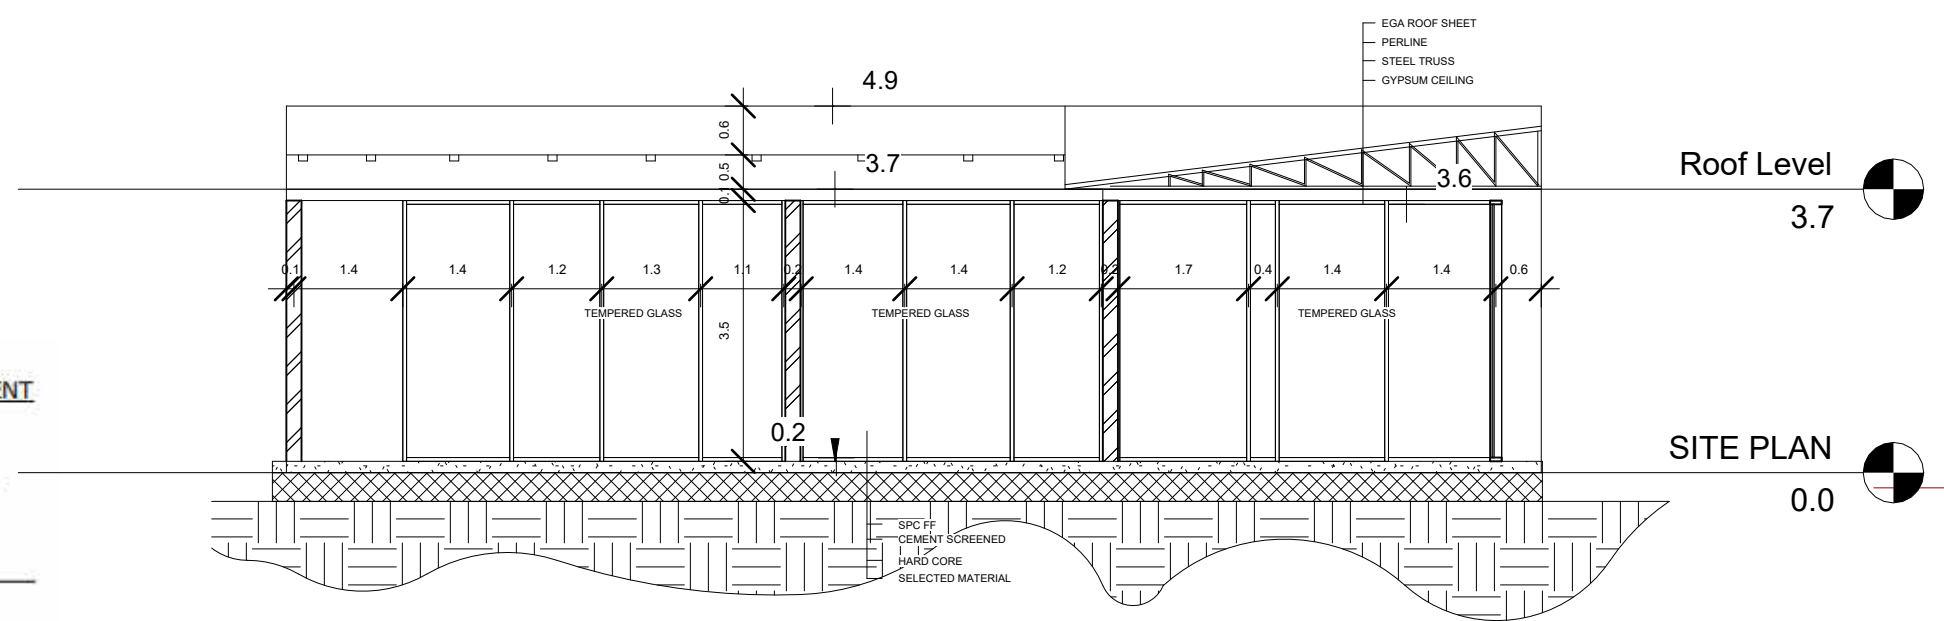


7 SECTION X
1 : 100

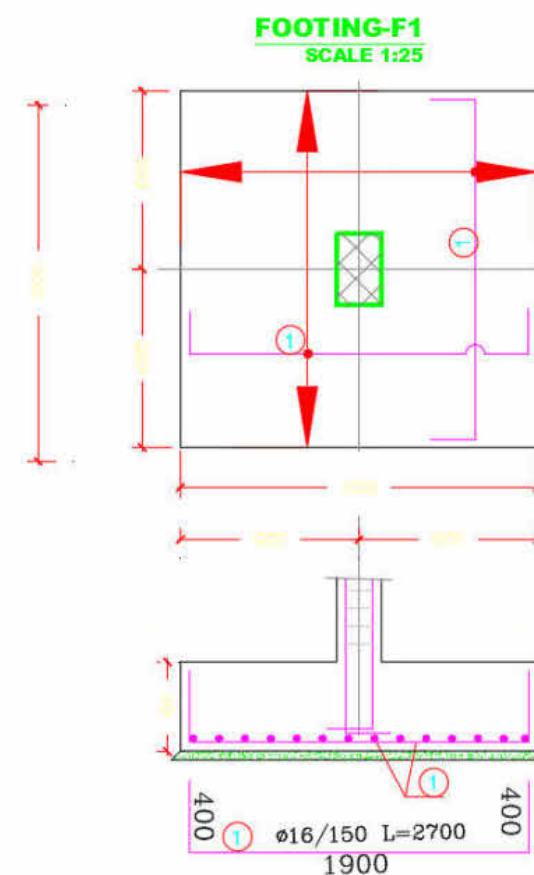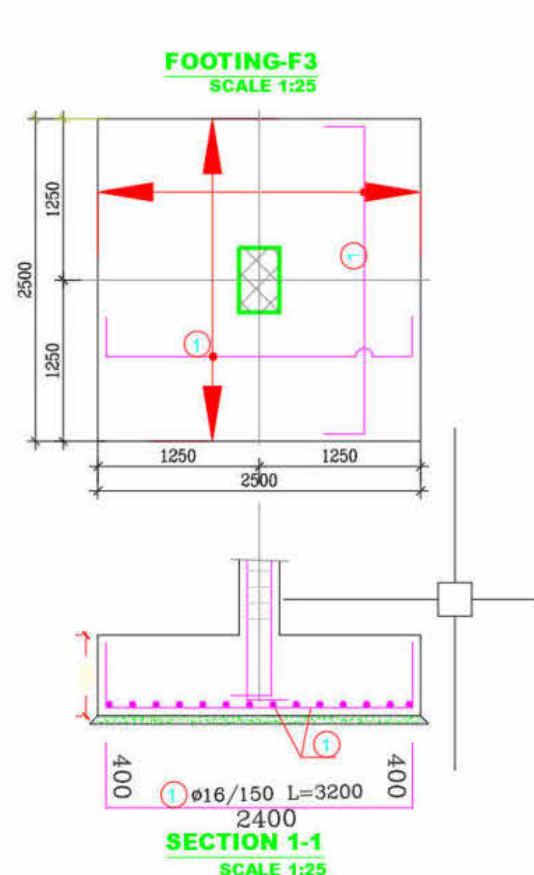


DETAIL DRAWINGS

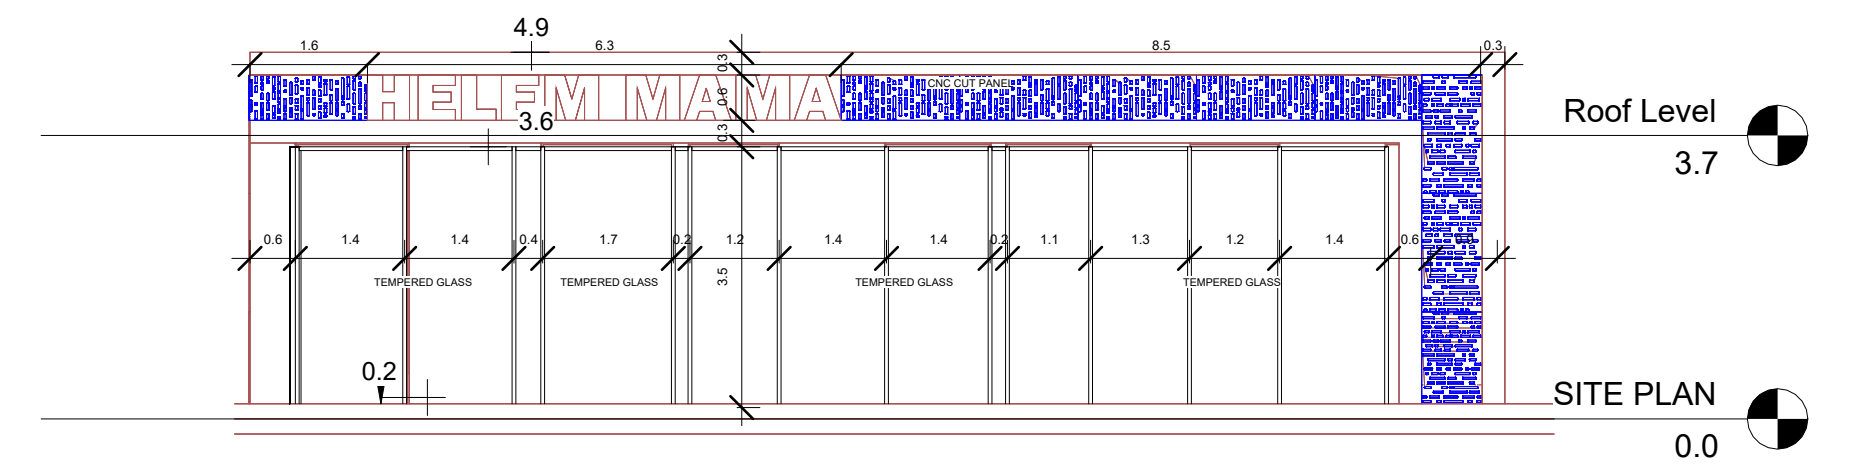


1 FRONT ELEVATION
1 : 100

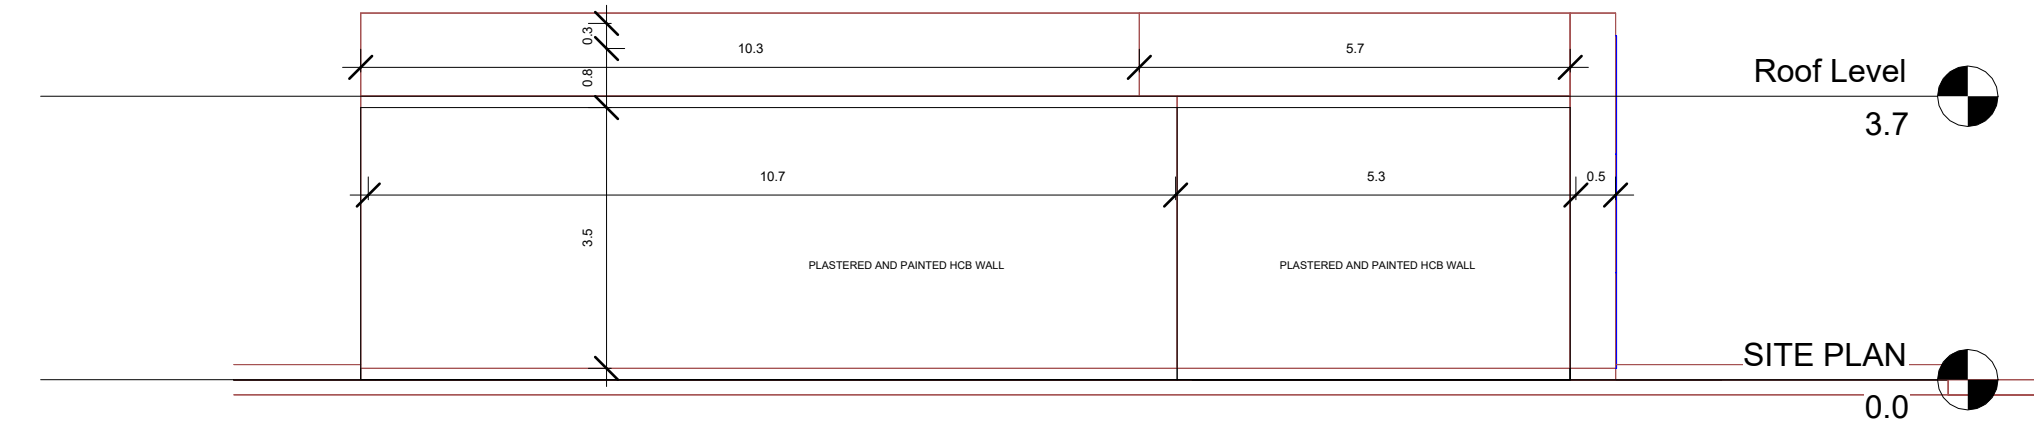


2 REAR ELEVATION
1 : 100

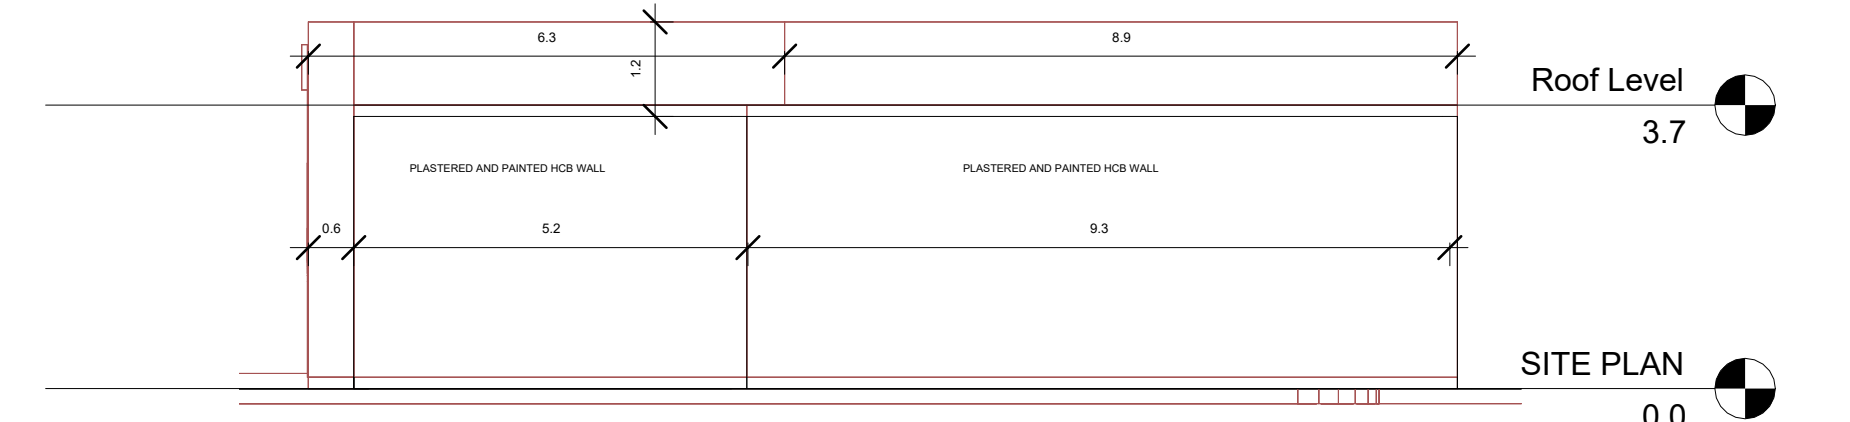


3 RIGHT ELEVATION
1 : 100

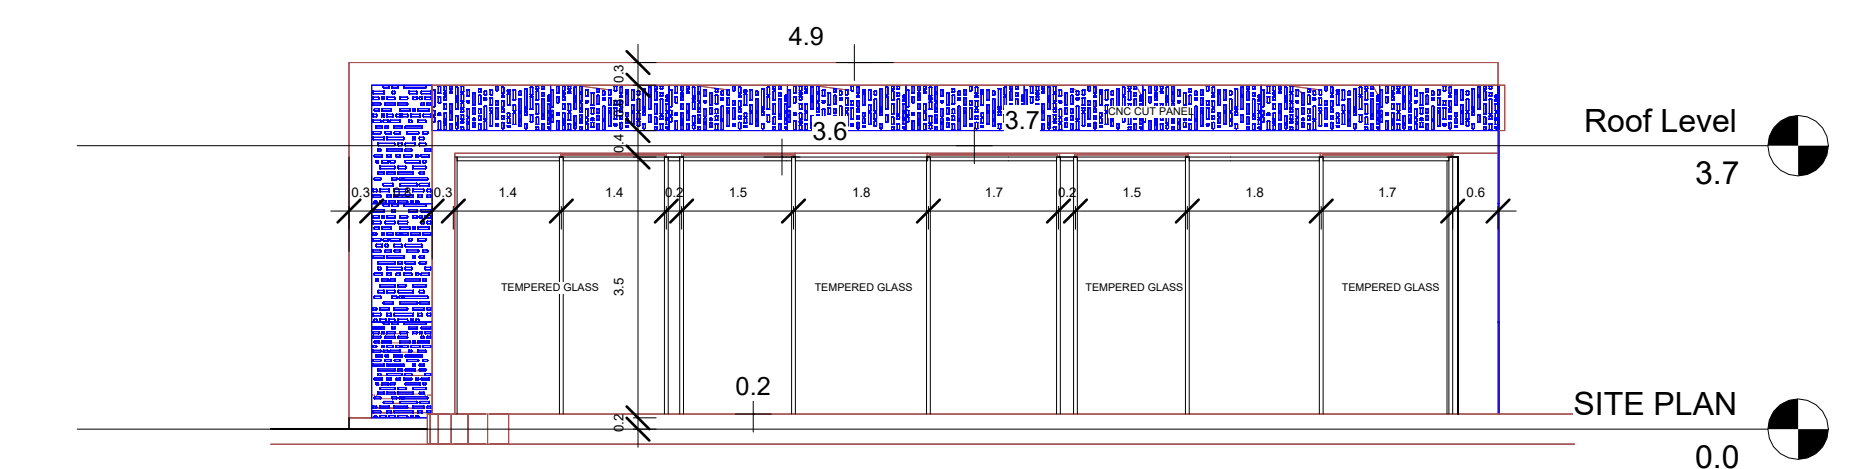

4 LEFT ELEVATION
1 : 100

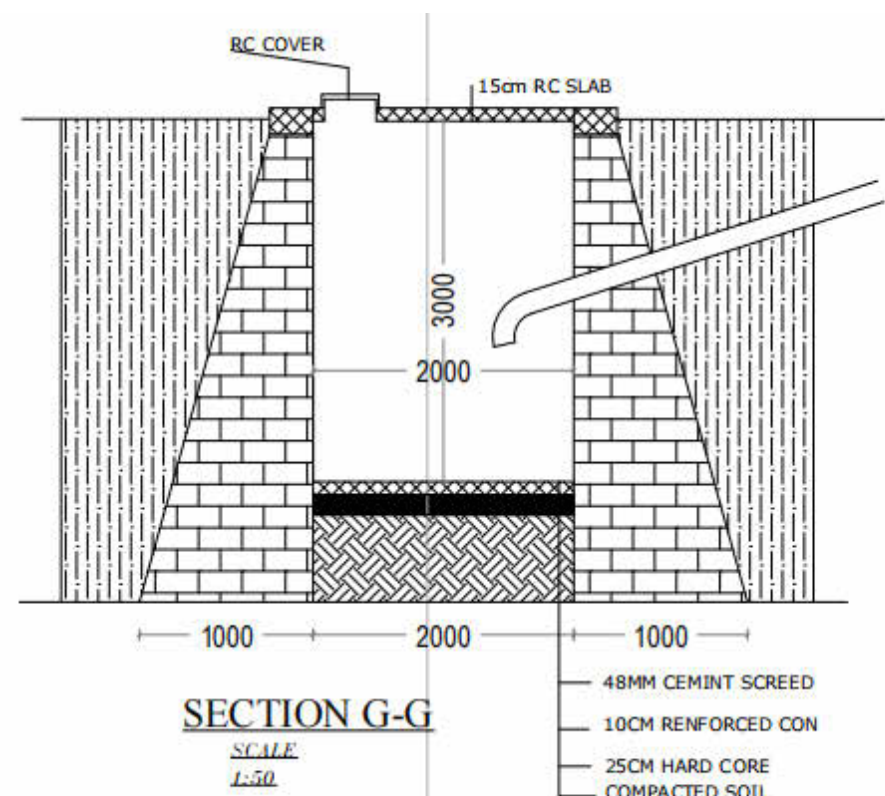


BEAM DETAIL ON AXIS 1, 2, A & B

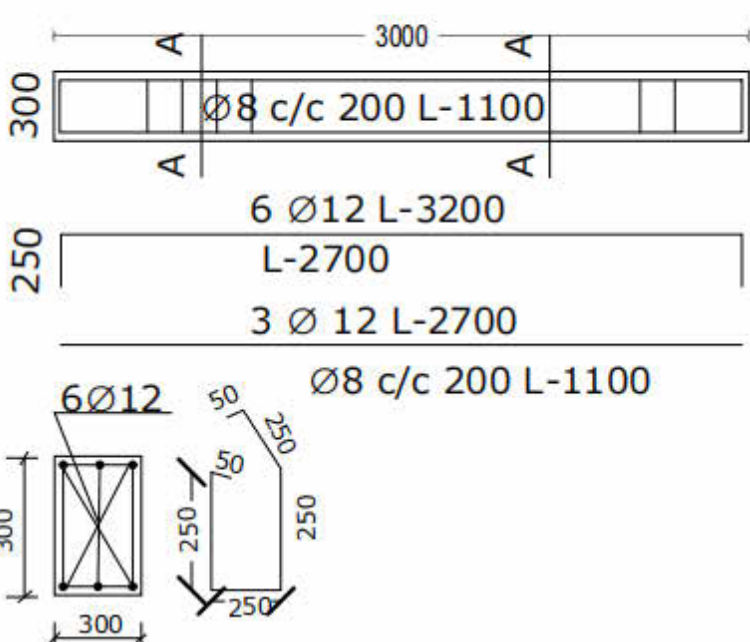


SECTION A-A
SCALE 1:25

Genekibo Architects			
CLIENT	FATUMA ABDU		
LOCATION	SEMERA		
	NAME	REG.	
DESIGN BY	HABIB AHMED	GAR/88764	
CHECKED BY	MOHAMMED ABDELAH	GAR/96320	
APPROVED BY	MOHAMMED ABDELAH	GAR/96320	
DESIGN REF.			
PROJECT	Shoping Center		
DRAWING TITLE			
SCALE	AS INDICATED		
DATE	6/09/2026		

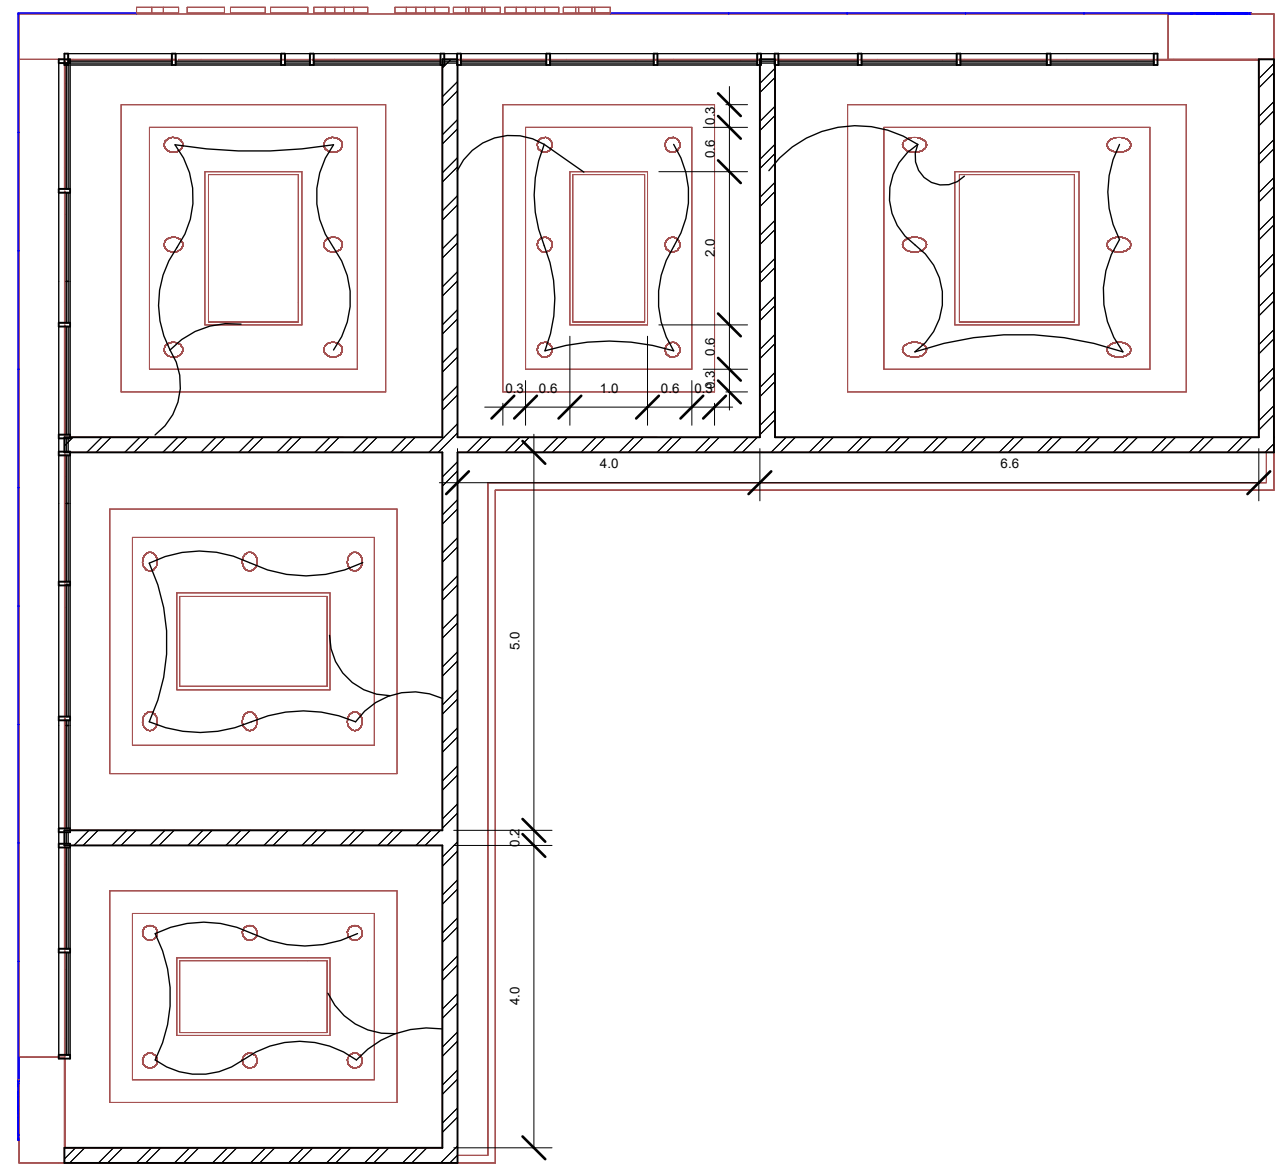

1
INSTALATION OF LIGHT
AND SWITCH

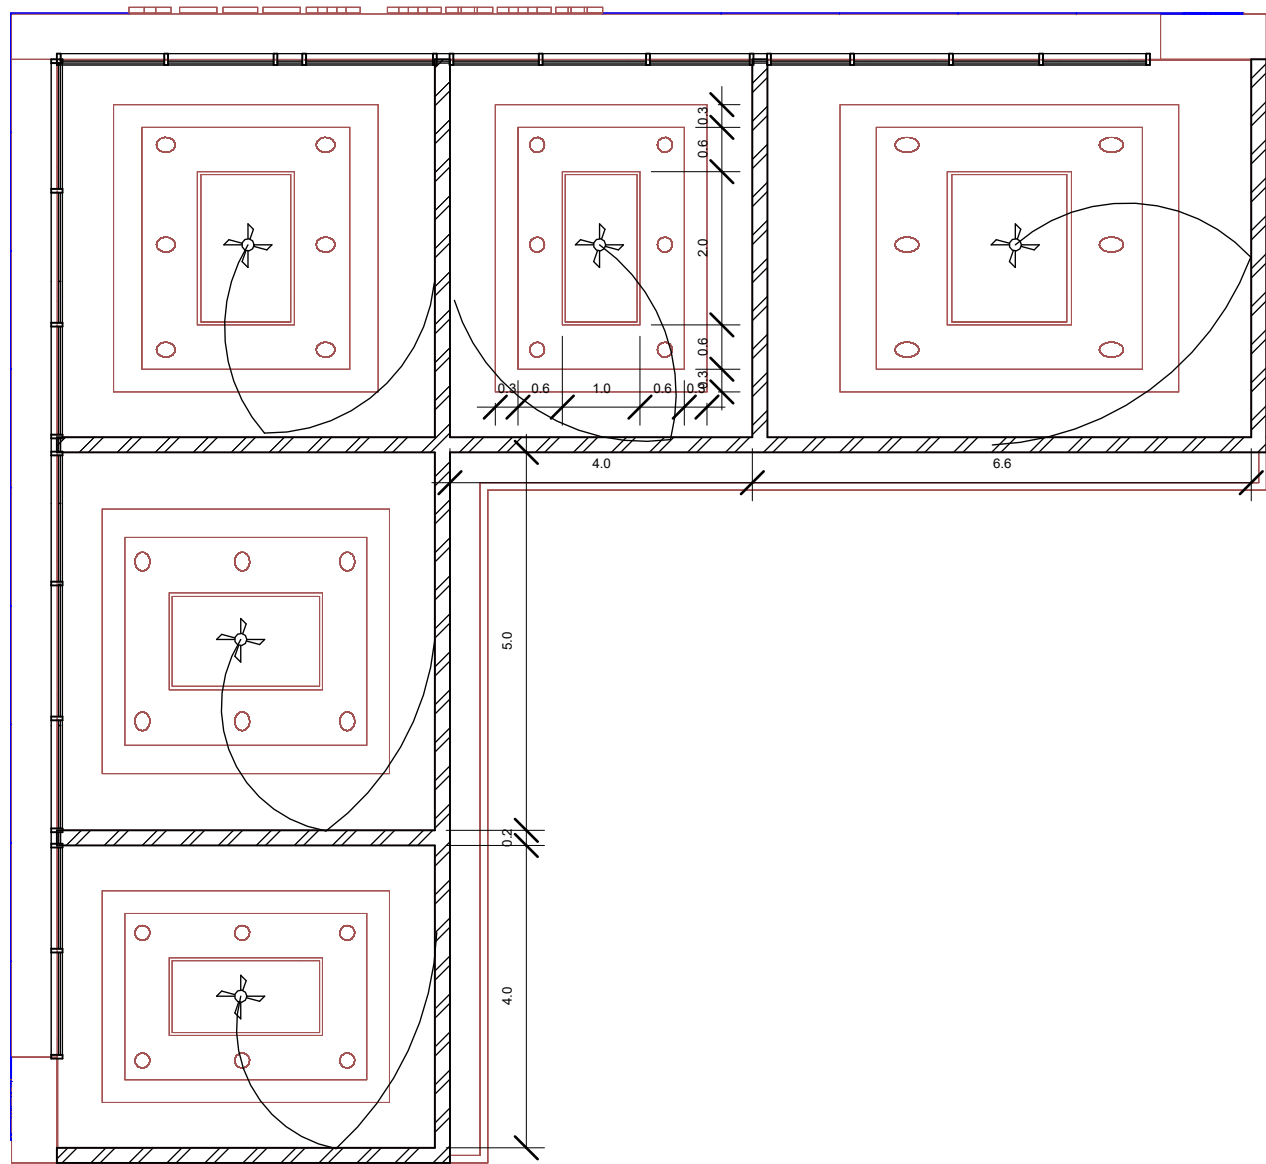

2
INSTALLATION OF SOCHET
AND FAN

LEGEND

SURFACE MOUNTED DOWN LIGHT

SURFACE MOUNTED WALL LIGHT

PEDESTAL & POST TOP LIGHT

RECESSED MOUNTED SINGLE SWITCH

RECESSED MOUNTED TWO-WAY SWITCH

RECESSED MOUNTED DOUBLE SWITCH

RECESSED MOUNTED SINGLE SOCKET OUTLET

RECESSED MOUNTED TV OUTLET

RECESSED MOUNTED WATER PROOF SINGLE SOCKET OUTLET

RECESSED MOUNTED HEATER OUTLET

Distribution Board

Wall Mounted light Fitting

TV Outlet

TV Coaxial Cable inside conduit of Ø 19mm

Flush Mounted TV Terminal Box

Telephone Voice or Data Outlet RJ45 (Mounting Height @ 30cm FFFL)

Rack Mounted Telephone Terminal Box and/or Data Switch

Flush Mounted Telephone(Only Voice) Terminal Box

Data CAT 6A Cable inside conduit of Ø 19mm

DESCRIPTION	I(A)	A(mm)	P(KW)	Phases			Conduit dia.(mm²)
LIGHTING	1/10A	2x2.5	0.445	●			13
LIGHTING	1/10A	2x2.5	0.385		●		13
SOCKET OUTLET	1/16A	3x2.5	1.00			●	16
SOCKET OUTLET	1/16A	3x2.5	1.20	●			16
SOCKET OUTLET	1/16A	3x2.5	1.20		●		16

SDB-TERRACE

1

2

3

$P_{tot} = 1.58KW$

5x6MM²

3 x 32 A

LINE FROM

$P_{max} = 30.076kw$

25.68

DESCRIPTION	I(A)	A(mm)	P(KW)	Phases			Conduit dia.(mm²)
LIGHTING	1/10A	2x2.5	0.180	●			13
LIGHTING	1/10A	2x2.5	0.200		●		13
SOCKET OUTLET	1/16A	3x2.5	1.20			●	16
RESERVE							

$P_{tot} = 1.58KW$

$P_{max} = 1.264KW$

(D.F.=0.8)

Genekibo Architects			
CLIENT	FATUMA ABDU		
LOCATION	SEMERA		
	NAME	REG.	
DESIGN BY	HABIB AHMED	GAR/88764	
CHECKED BY	MOHAMMED ABDELAH	GAR/96320	
APPROVED BY	MOHAMMED ABDELAH	GAR/96320	
DESIGN REF.			
PROJECT	Shoping Center		
DRAWING TITLE	ELECTRICAL DRAWINGS		
SCALE	AS INDICATED		
DATE	6/09/2026		